

版权保护。严禁禁止在未获得明确授权的情况下下载、转发和复制本文档，利用及传播其内容。




冉昆真空科技（浙江）有限公司

公司/客户
项目描述 X-101 75KW液环罗茨机组
图号 2023-34-12014
设计 冉昆真空科技有限公司

制造商(公司) 冉昆真空科技有限公司
地址 An der alten Ziegelei 2
电话 +49 (0)2173 - 39 64 - 0
项目名称 2023-34-12014-1
项目负责人 王经理

编辑日期： 2024/1/17 创建者： 虎存山 审核人： 王经理 页数 17

			项目名称 2023-34-12014-1	项目编号 2023-34-12014	冉昆真空科技有限公司 	首页			=	&EAA	
			X-101 75KW液环罗茨机组	图号							
										+	页 1
修改	日期	姓名	创建者 虎存山	批准人		日期 2021/3/30	校对 EPL			页数 1 从 17	

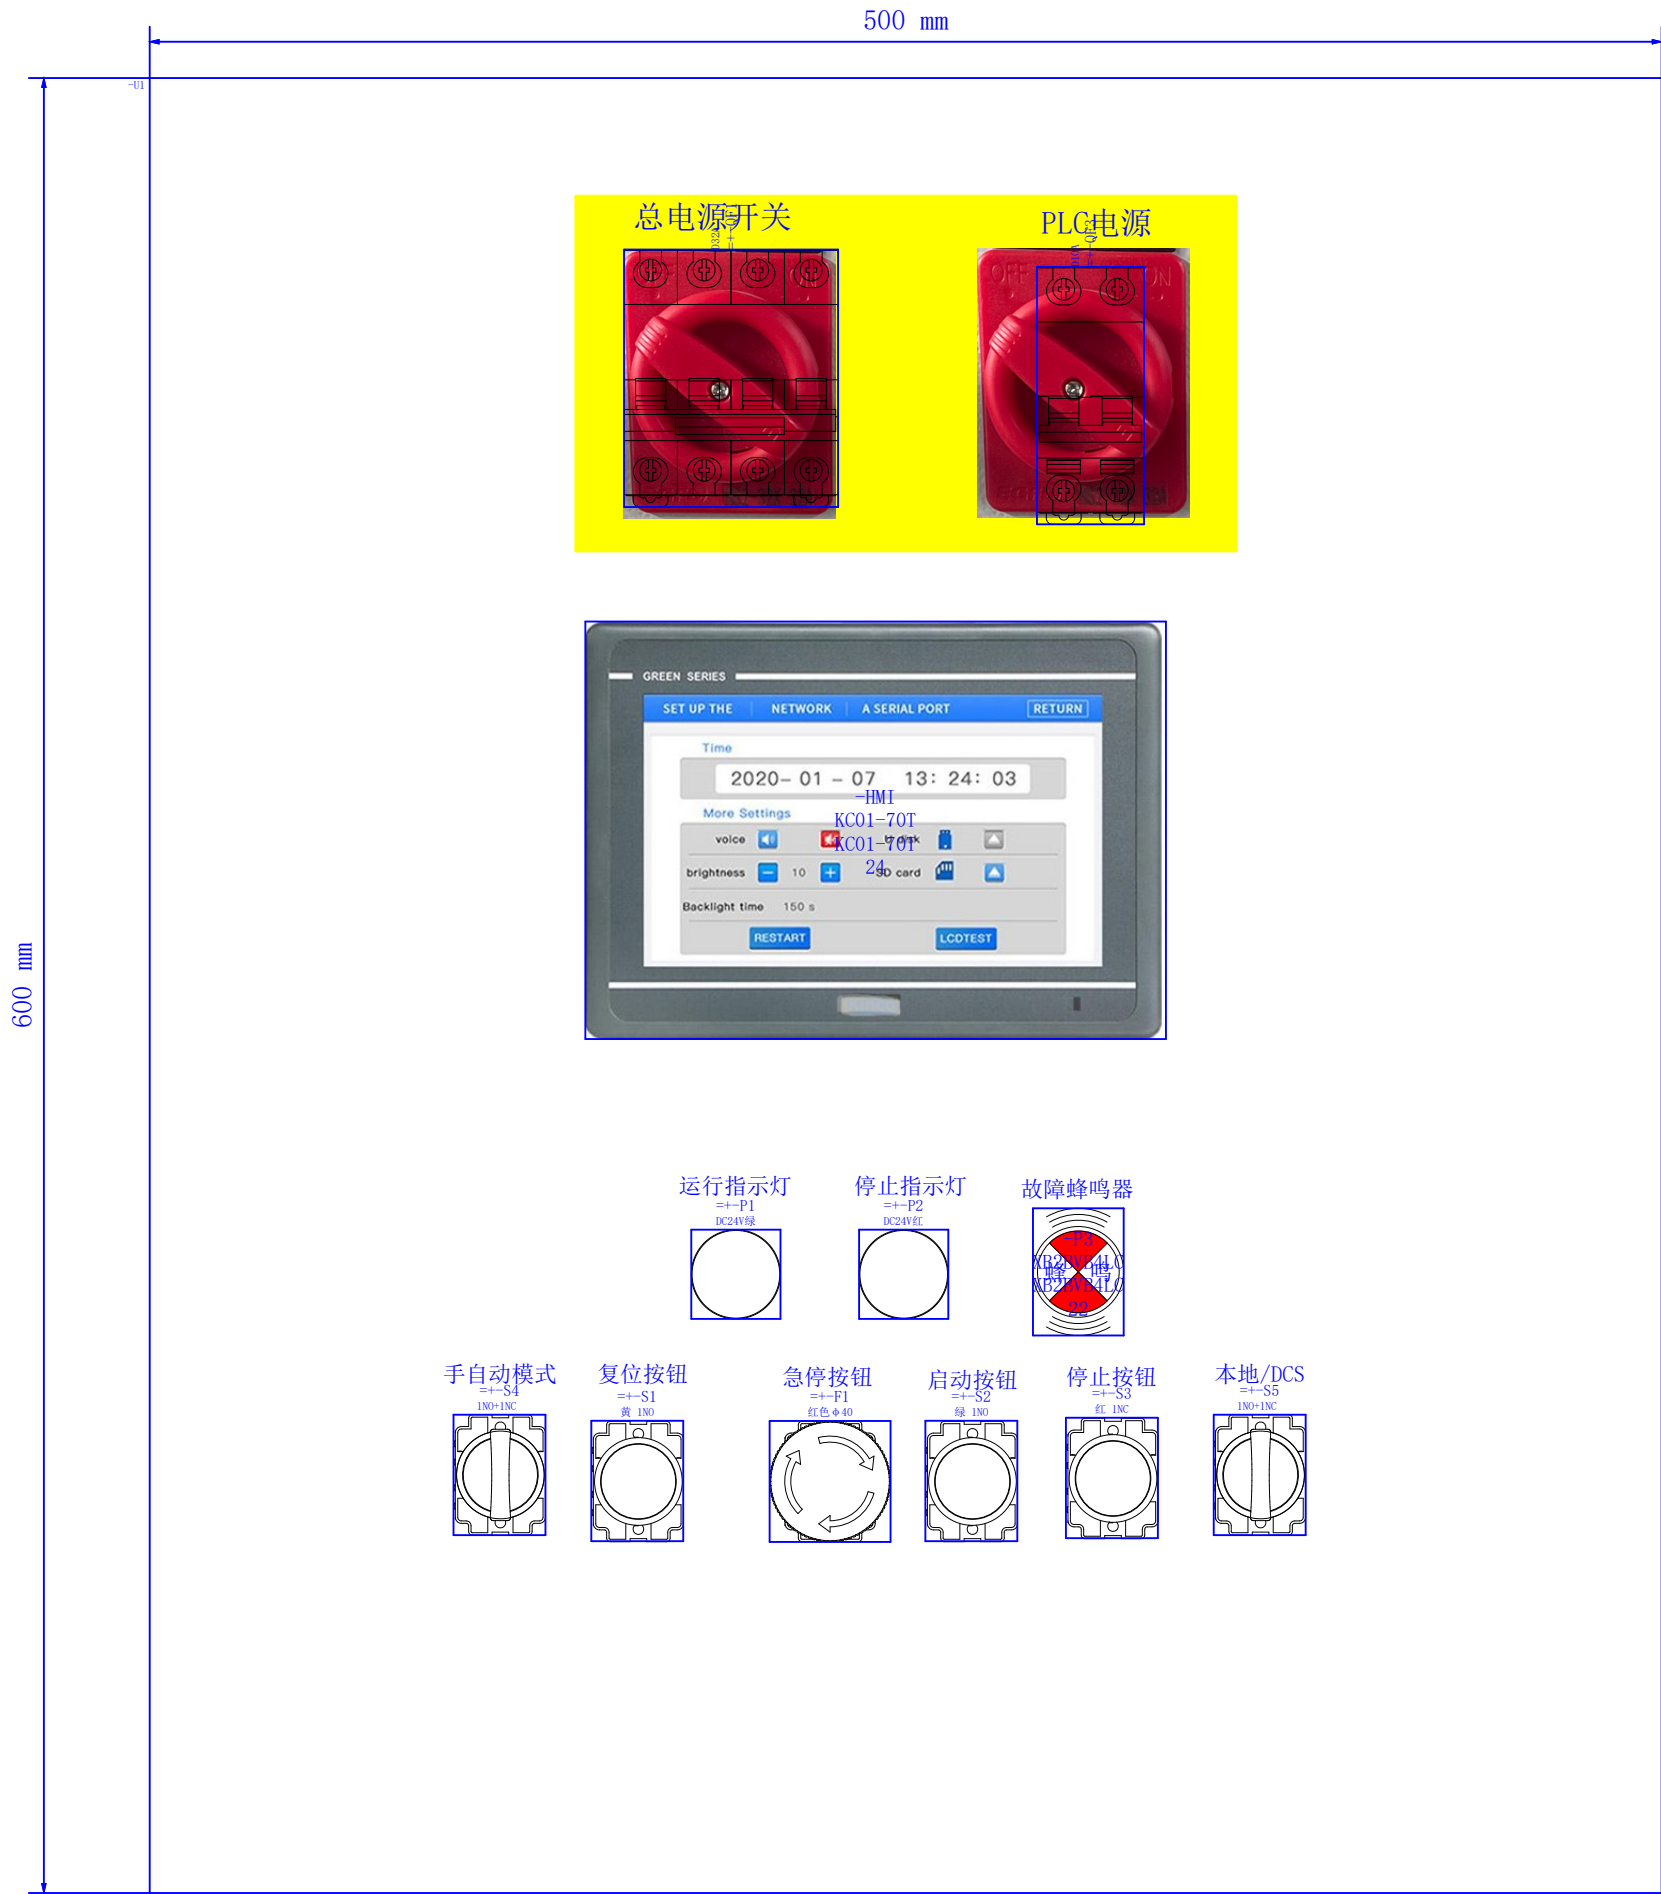


机柜尺寸:	500*600*300
机柜材质:	铝（根据实际情况定）
安装板尺寸:	420*520*3
固定方式:	背部
底部开孔	G1.5寸1个, G1寸2个, G3/4寸16个
防爆等级	ExDIIBT4
额定电压:	380V
额定电流:	5A
额定功率:	2KW
控制电压:	24V
断路器:	吊装安装方式
总电源:	IC65N 4P D32A 施耐德
PLC电源:	IC65N 2P 10A 施耐德
备注:	

箱柜设备清单

序号	设备标识符	型号	规格
1	QF1	SE. A9F19432	D32A
2	QF3	SE. A9F19210	D10A
3	S1	平头按钮 黄	黄 1NO
4	S2	平头按钮 绿	绿 1NO
5	S3	平头按钮 红	红 1NC
6	S4	旋转开关	1NO+1NC
7	S5	旋转开关	1NO+1NC
8	P1	DC24V绿	DC24V绿
9	P2	DC24V红	DC24V红
10	P3	XB2BVB4LC	24V无灯 持续
11	F1	急停	红色 φ 40
12	HMI	KC01-70T	


版权所有。未经许可，不得复制或传播其内容。

版权保护。严令禁止在未获得明确授权的情况下，转发和复制本文档，利用及传播其内容。

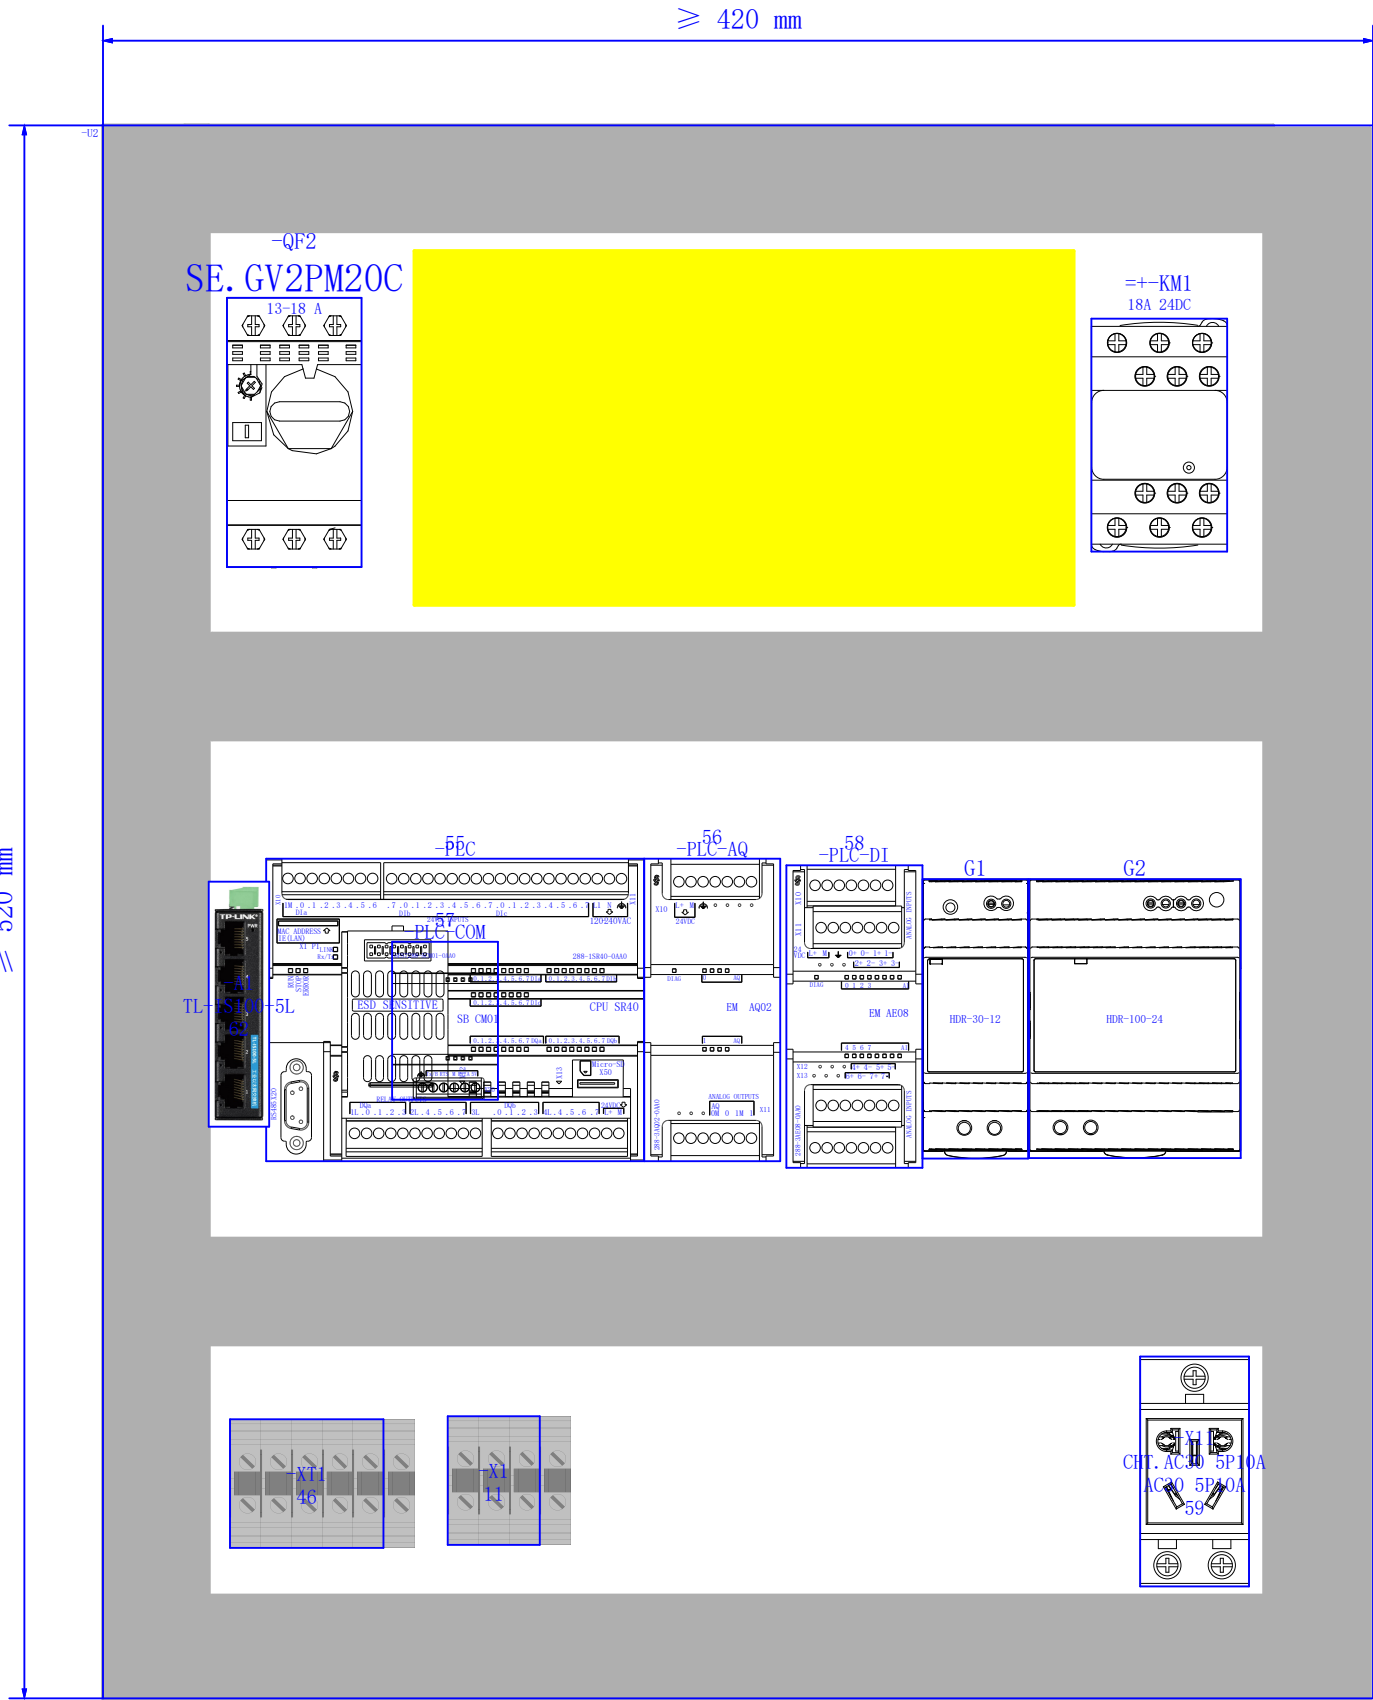

箱柜设备清单

序号	设备标识符	型号	规格
1	X1		
2	XT1		
3	QF2	SE. GV2PM20C	13-18 A
4	KM1	SE. LC1D18BDC	18A 24DC
5	PLC SIE.	6ES7288-1SR40-0AA0	
6	PLC-AQ SIE.	6ES7288-3AQ02-0AA0	
7	PLC-COM SIE.	6ES7288-5CM01-0AA0	
8	PLC-DS SIE.	6ES7288-3AE08-0AA0	
9	X11	CHT. AC30 5P10A	10A
10	G1	MW. HDR-30-12	HDR-30-12
11	G2	MW. HDR-100-24	HDR-100-24

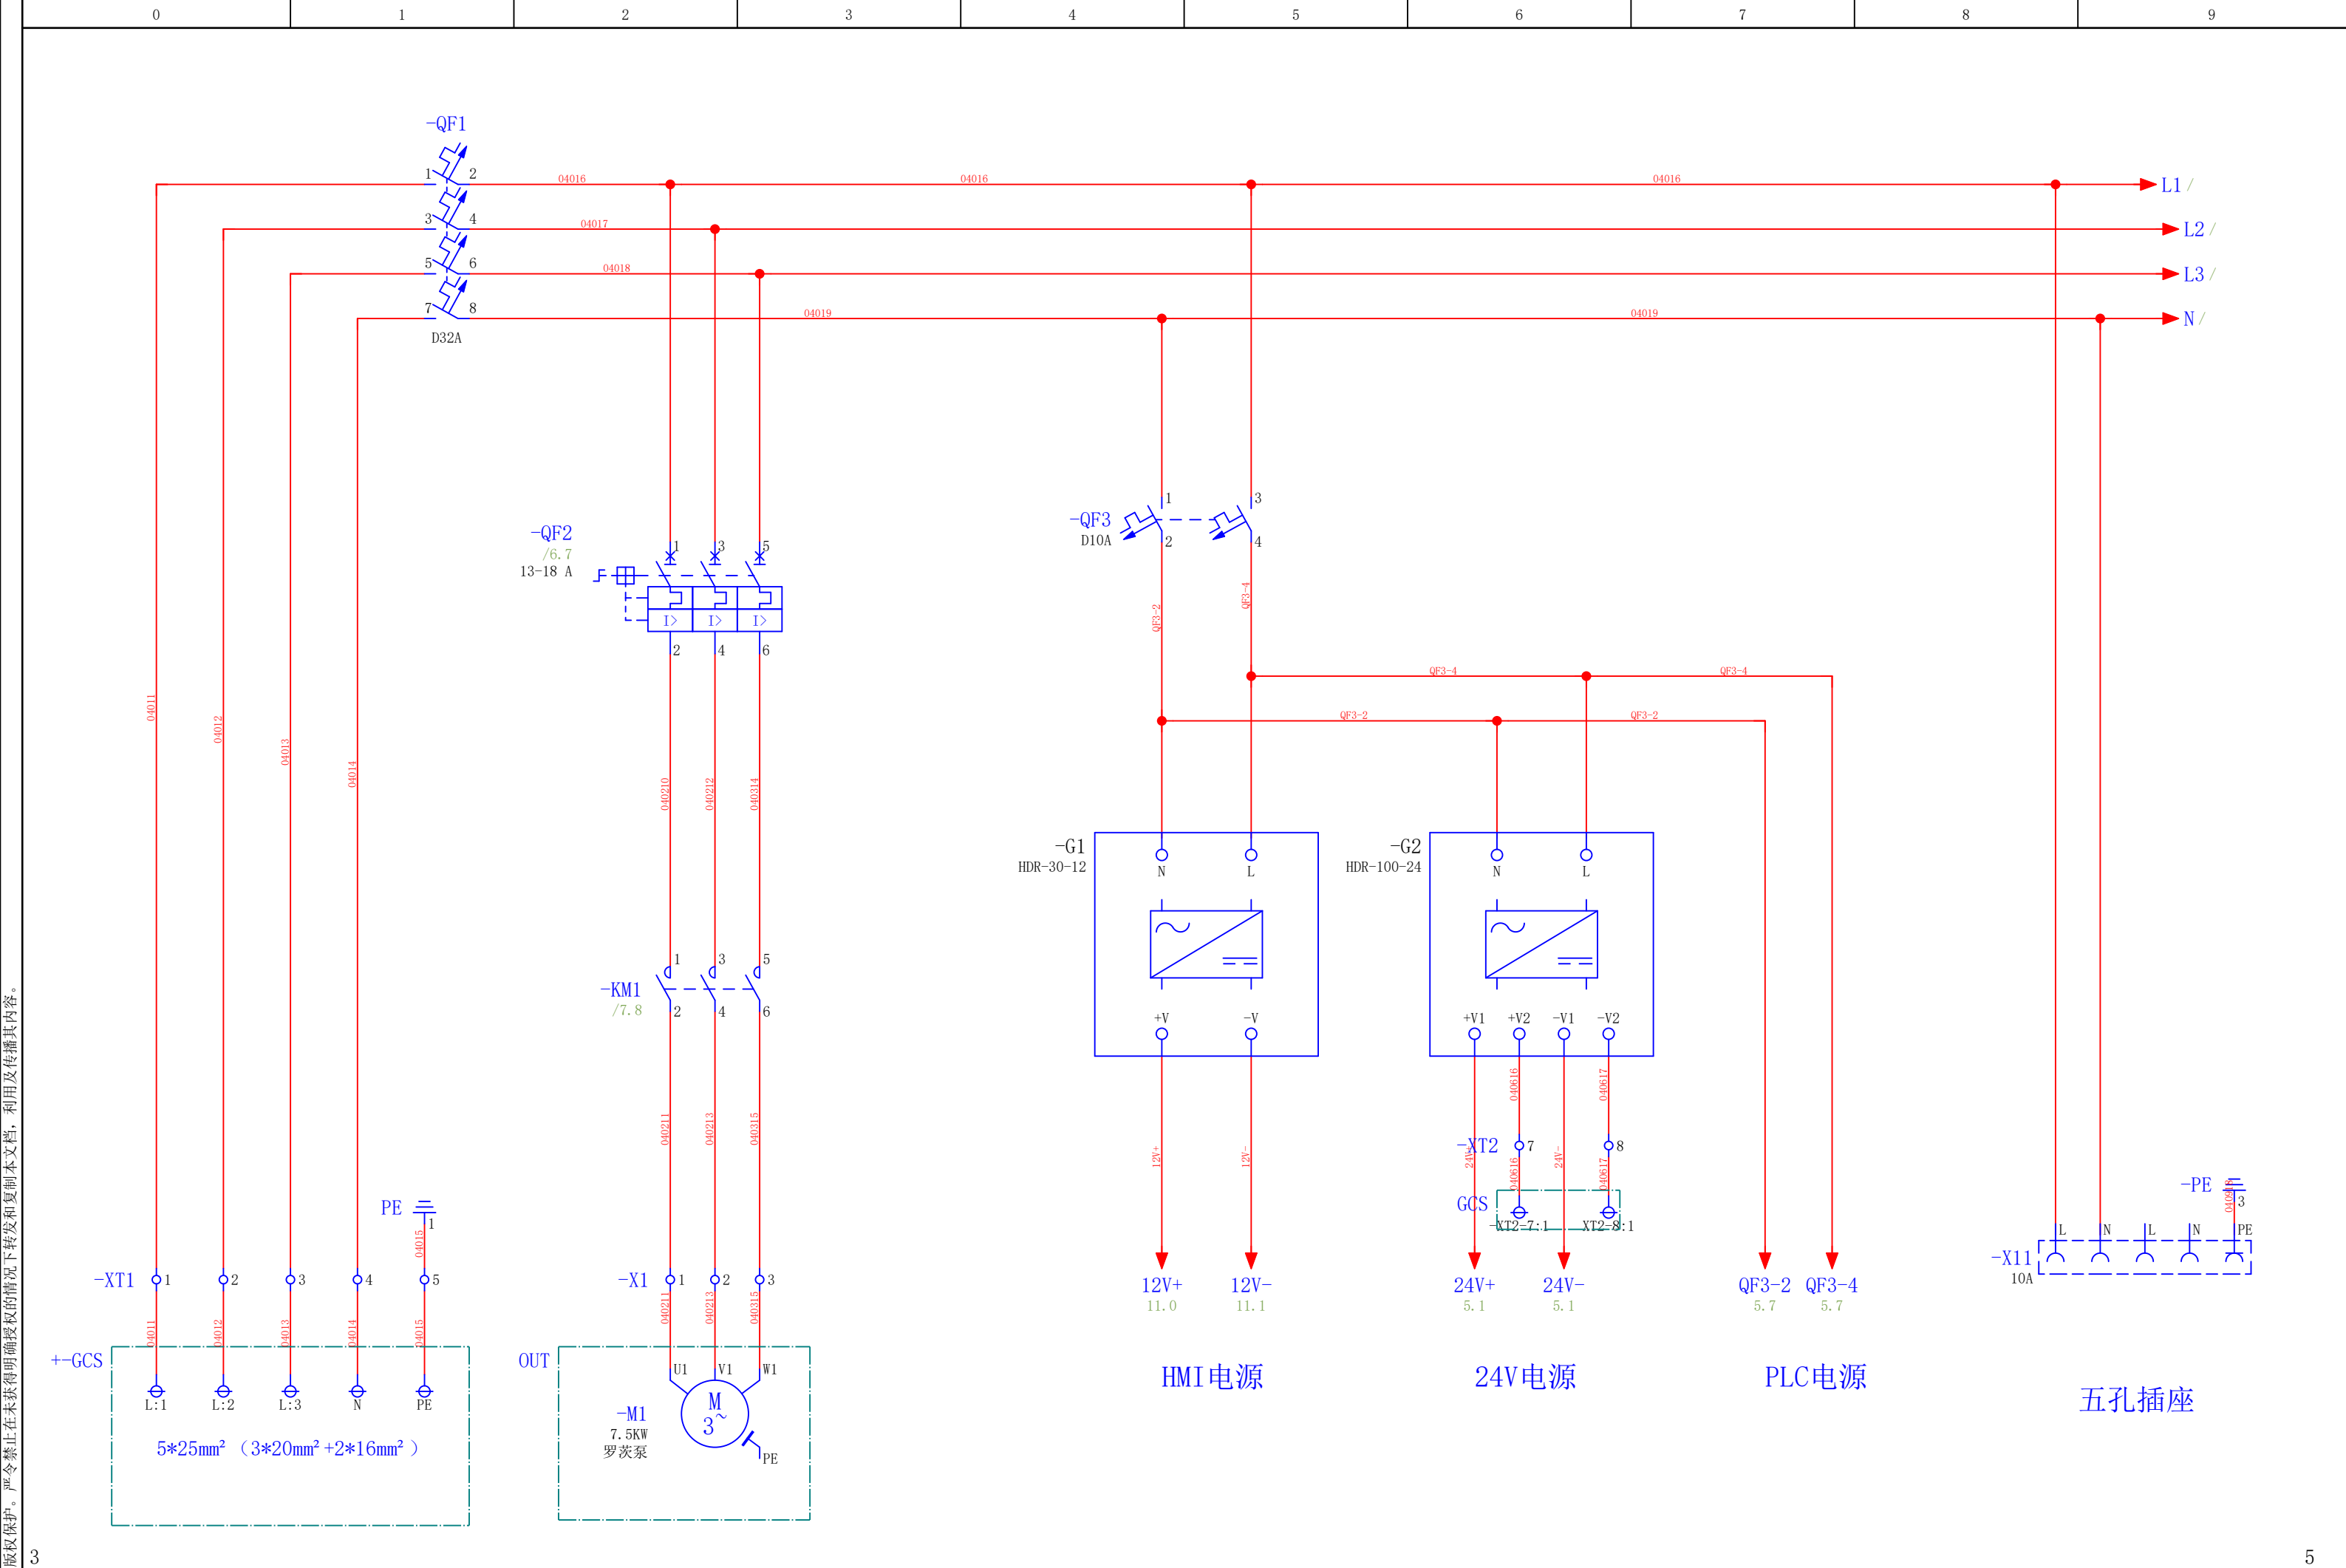


版权保护。严令禁止在未获得明确授权的情况下转发和复制本文档，利用及传播其内容。


			项目名称	2023-34-12014-1	项目编号	冉昆真空科技有限公司 	主回路			=	&EAA
			X-101 75KW液环罗茨机组		2023-34-12014						
					图号					+	页
修改	日期	姓名	创建者	虎存山	批准人		日期	2024/1/17	校对	虎存山	页数



页数	5	从	17
----	---	---	----

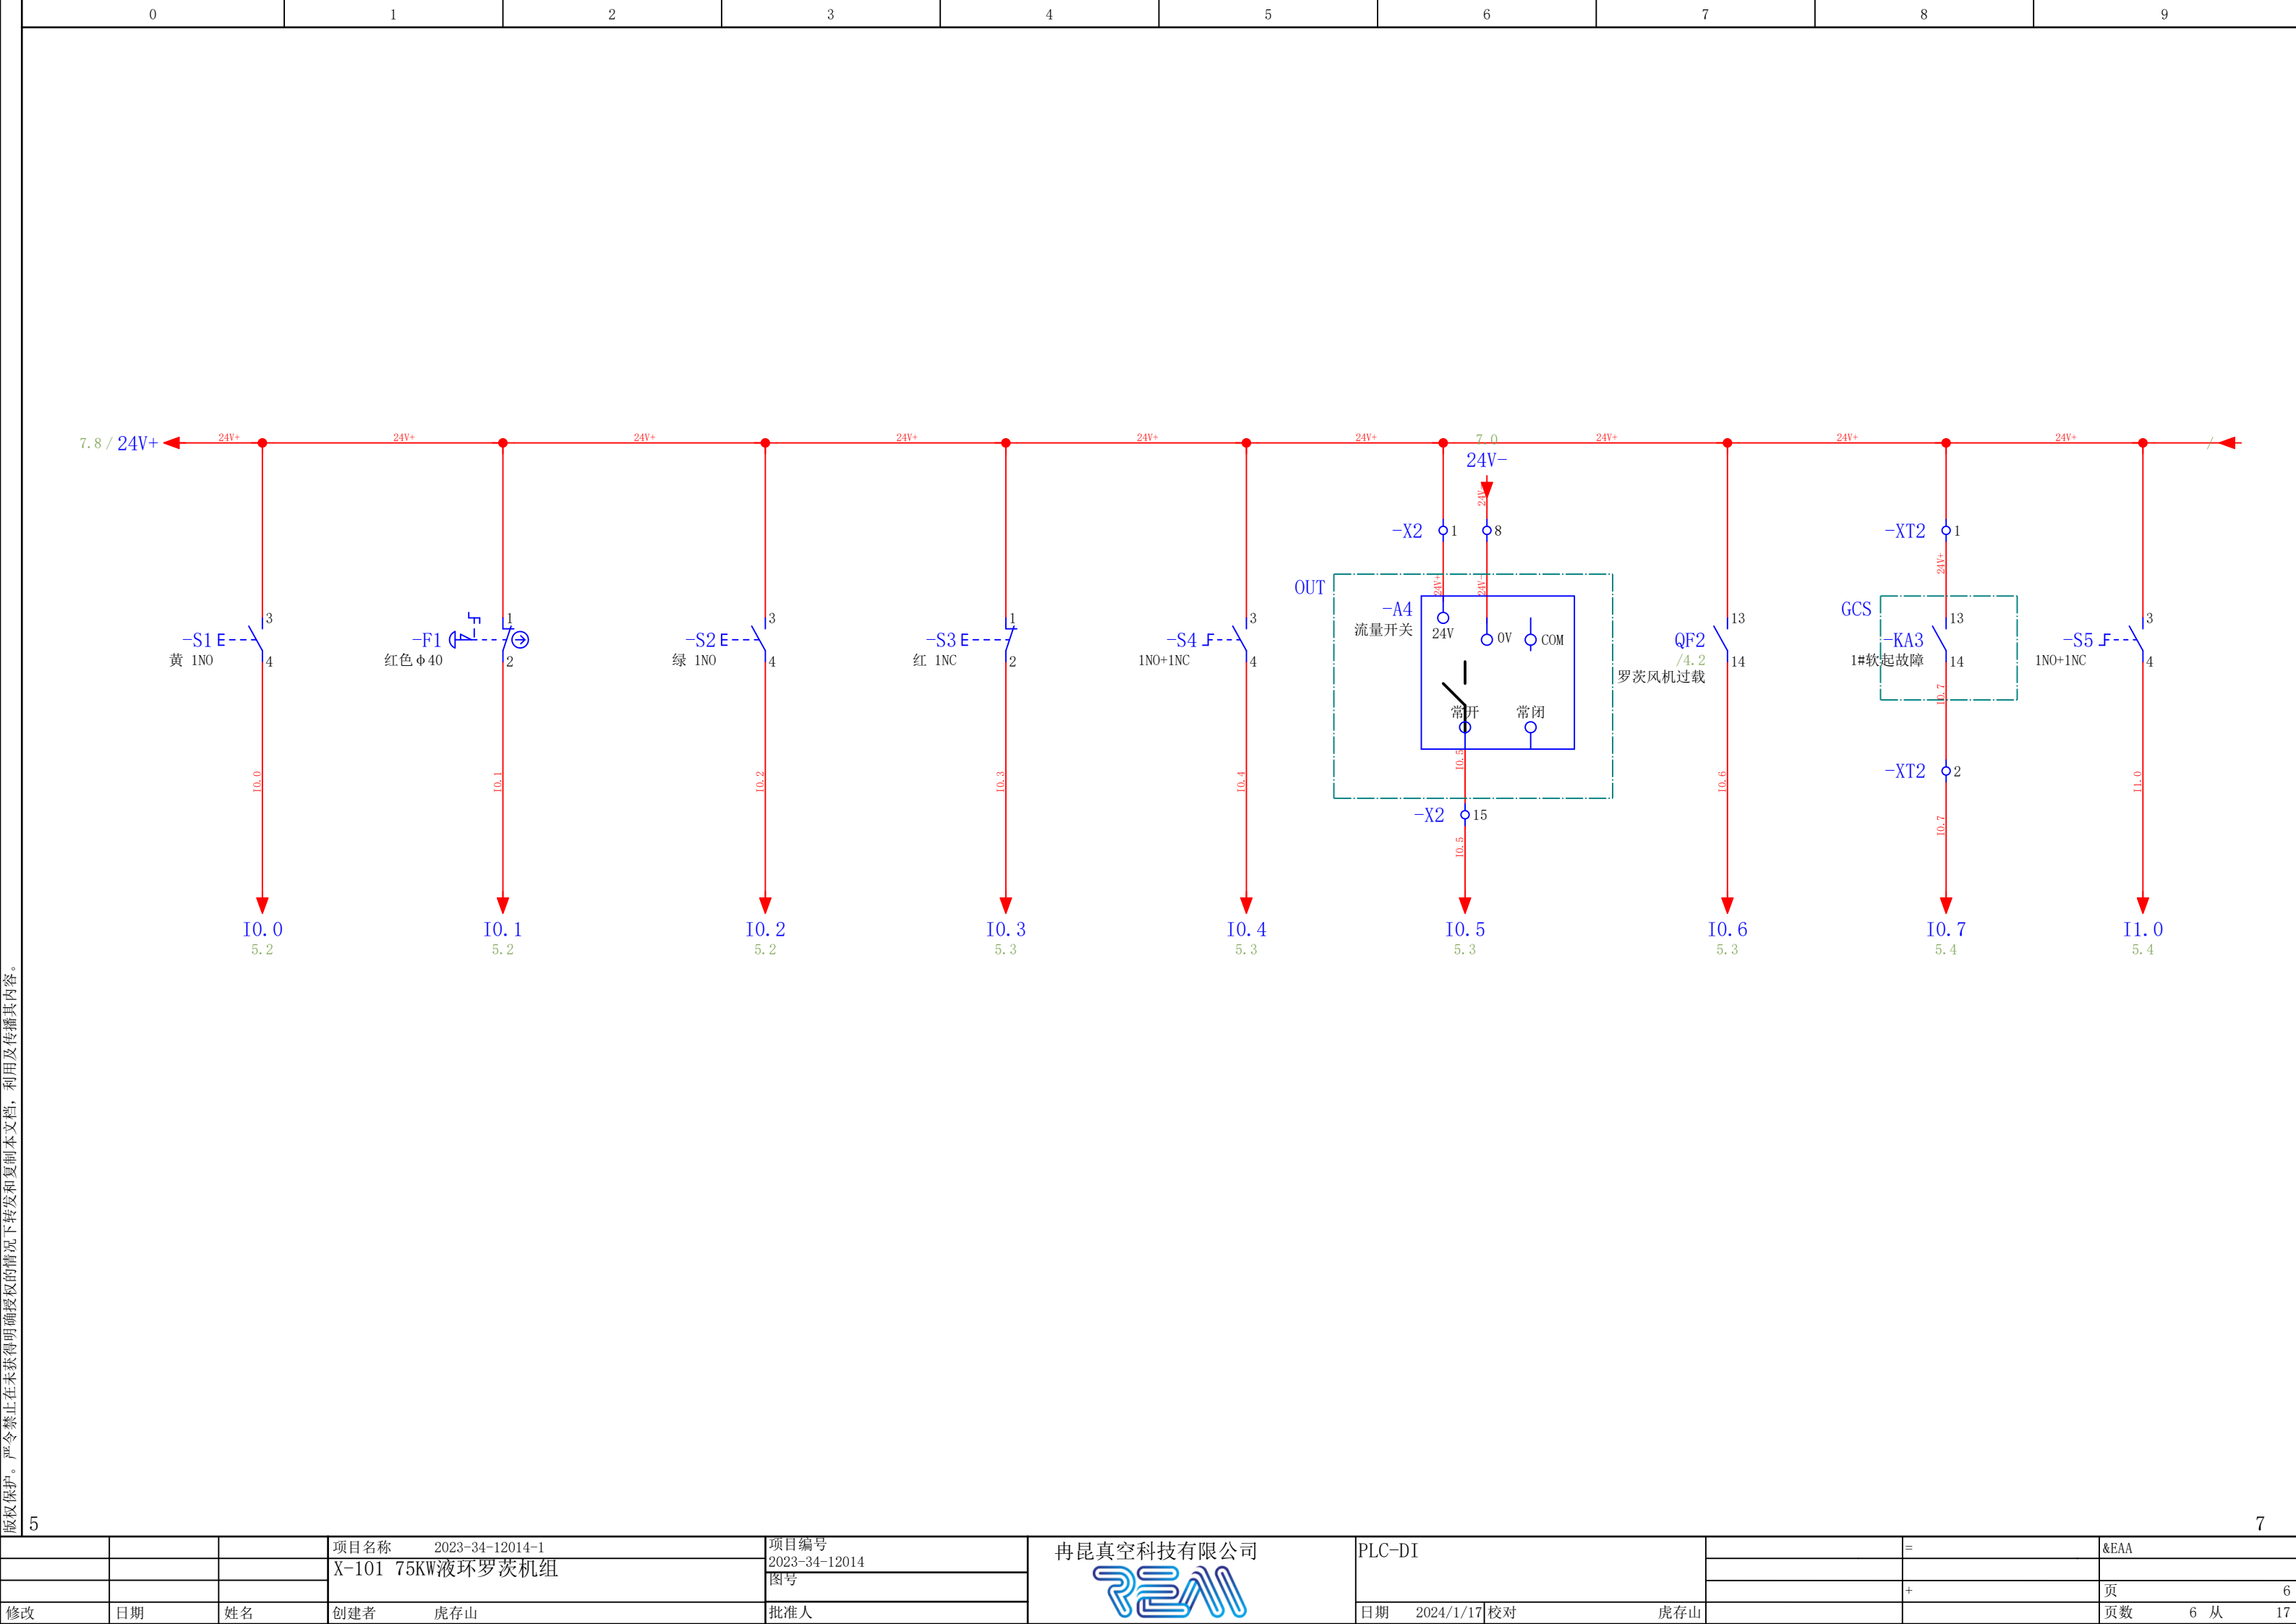



5
版权保护。严令禁止在未获得明确授权的情况下转发和复制本文档，利用及传播其内容。

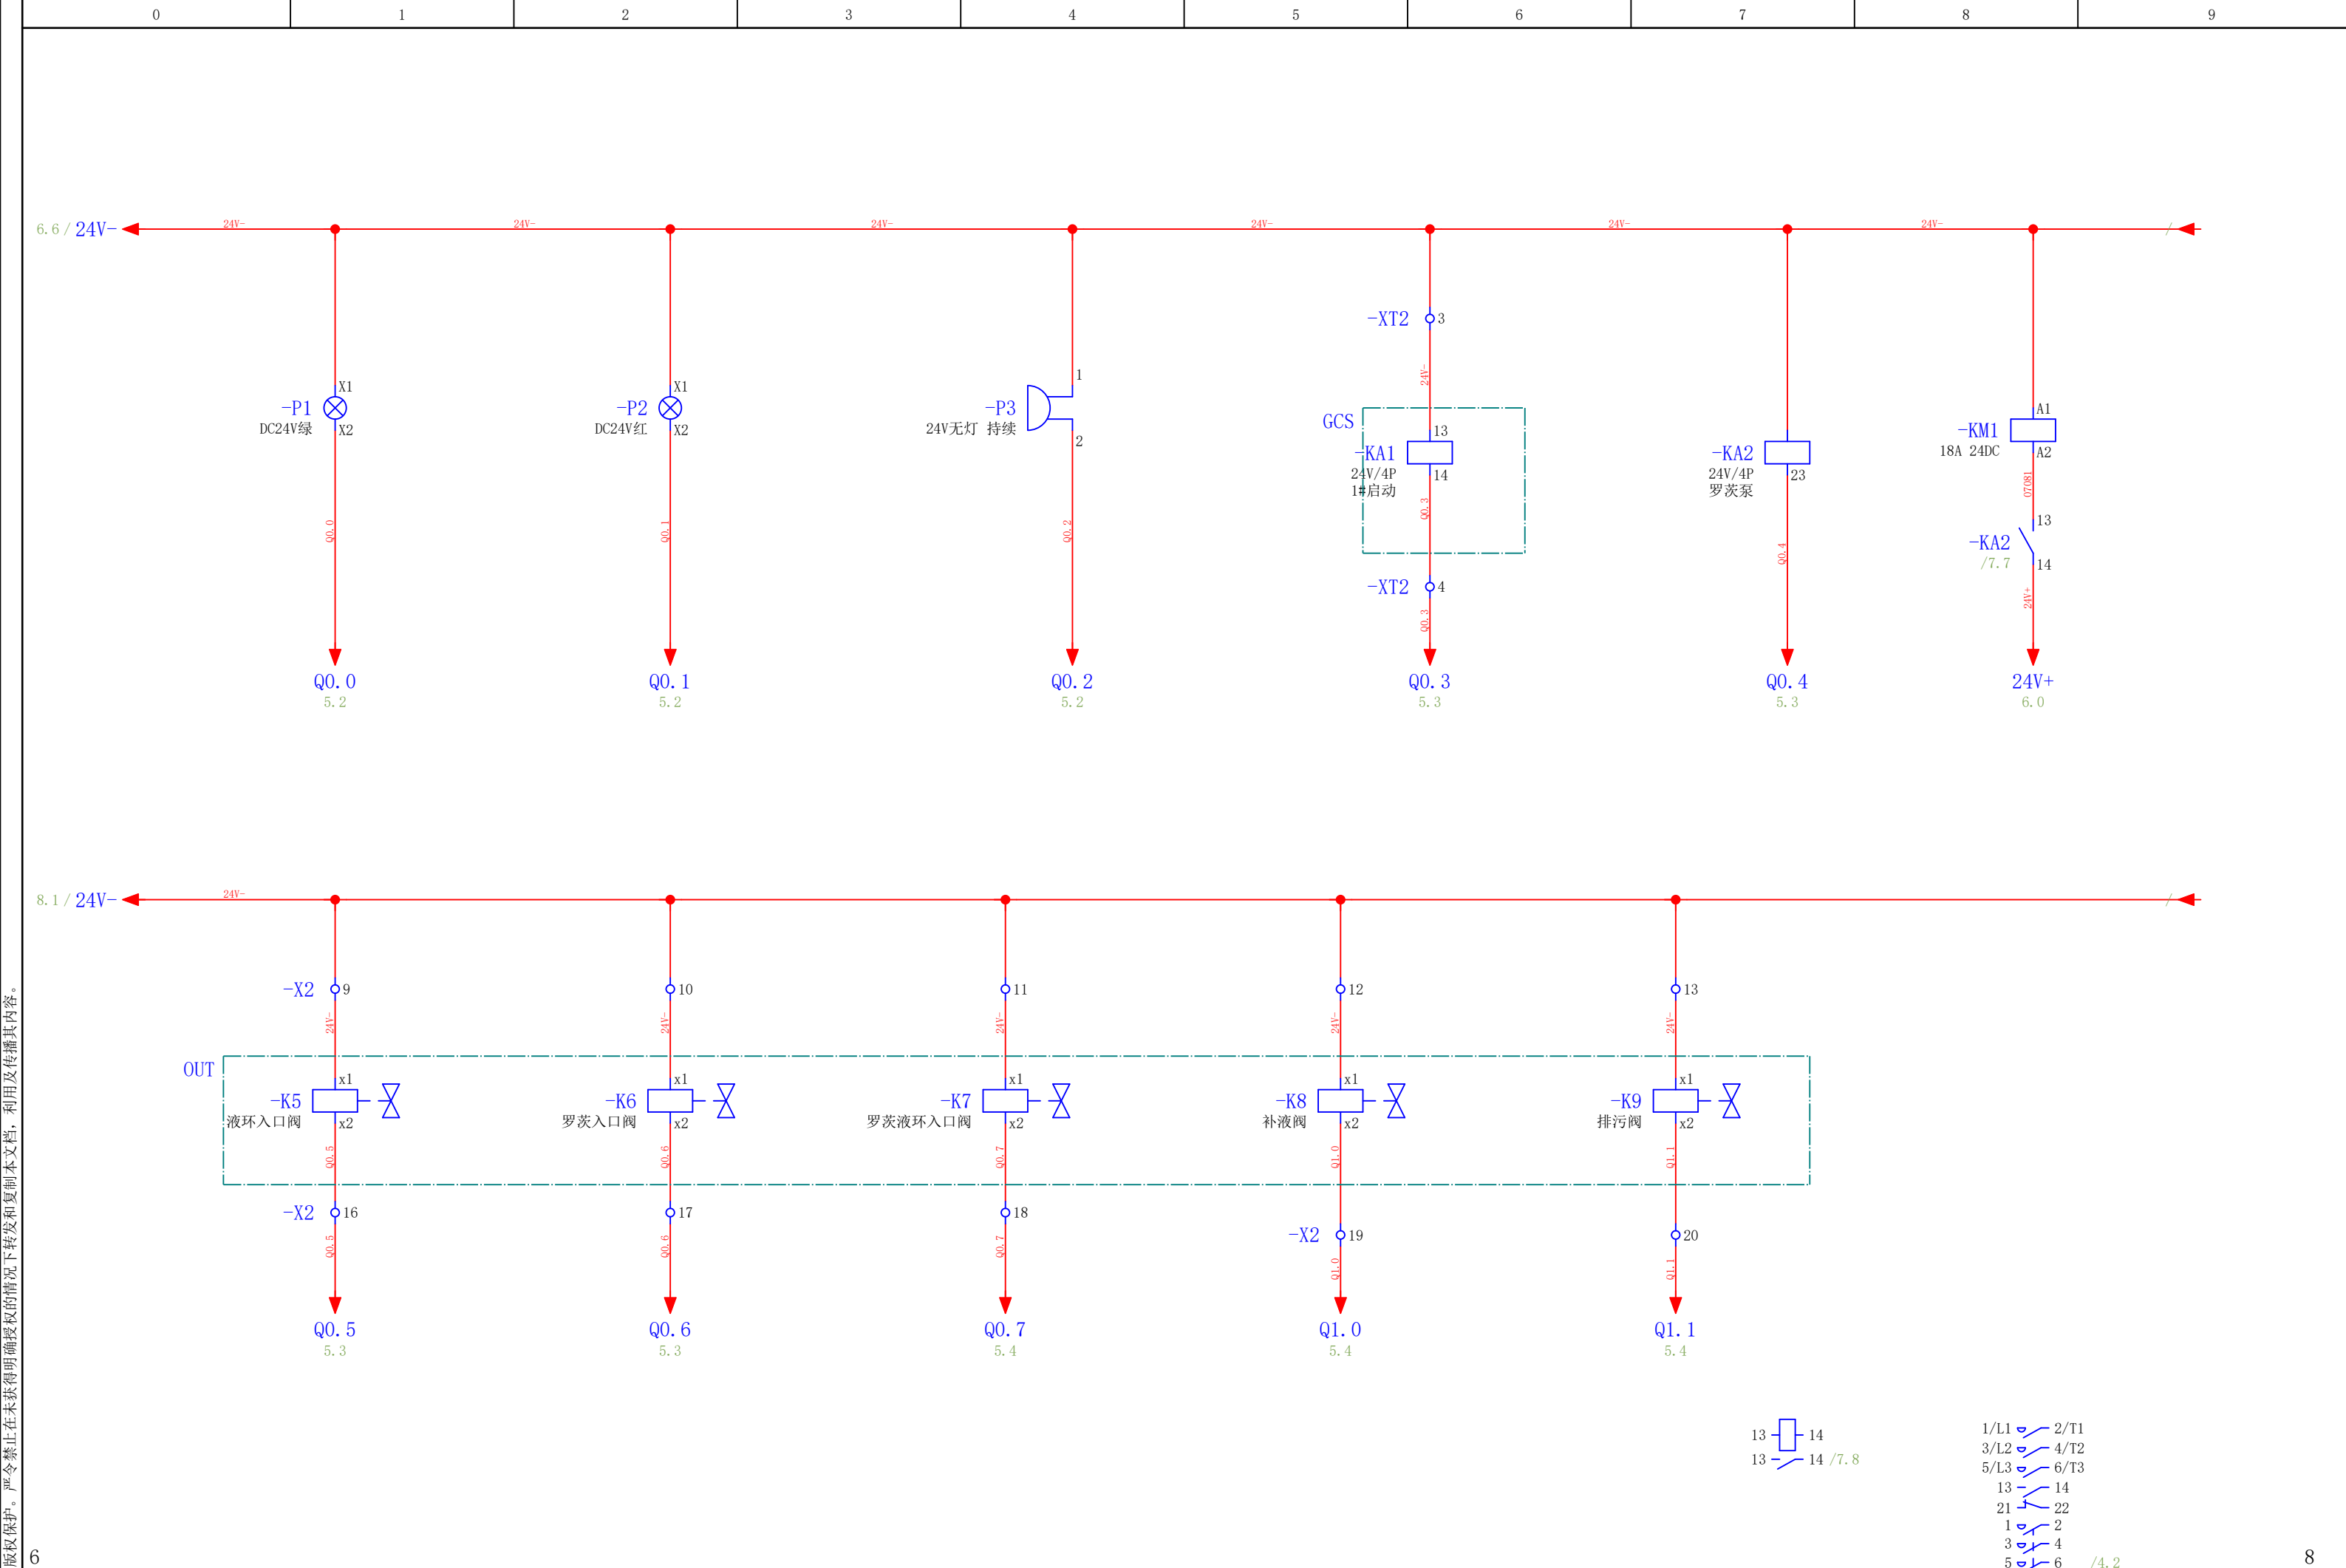


版权所有。严禁禁止在未获得明确授权的情况下转发和复制本文档，利用及传播其内容。


			项目名称	2023-34-12014-1	项目编号	冉昆真空科技有限公司 	PLC-D0			=	&EAA
			X-101 75KW液环罗茨机组		2023-34-12014						
					图号					+	页 7
修改	日期	姓名	创建者	虎存山	批准人		日期	2024/1/17	校对	虎存山	页数 7 从 17

7
版权保护。严令禁止在未获得明确授权的情况下，转发和复制本文档，利用及传播其内容。

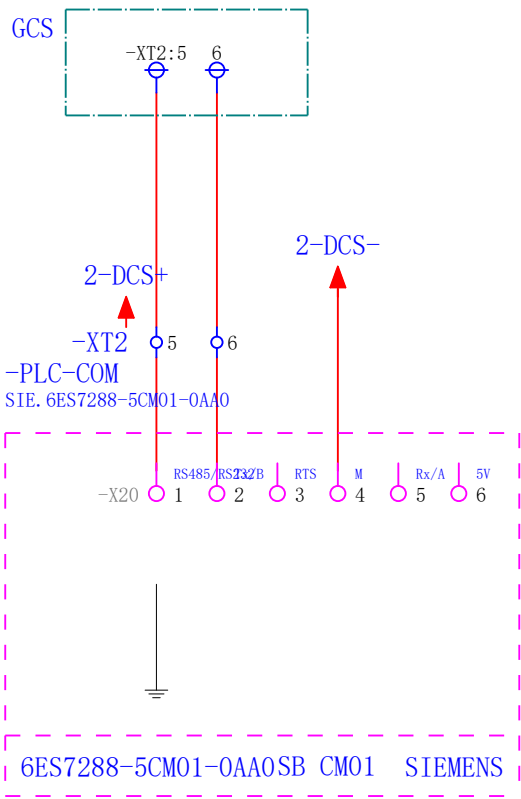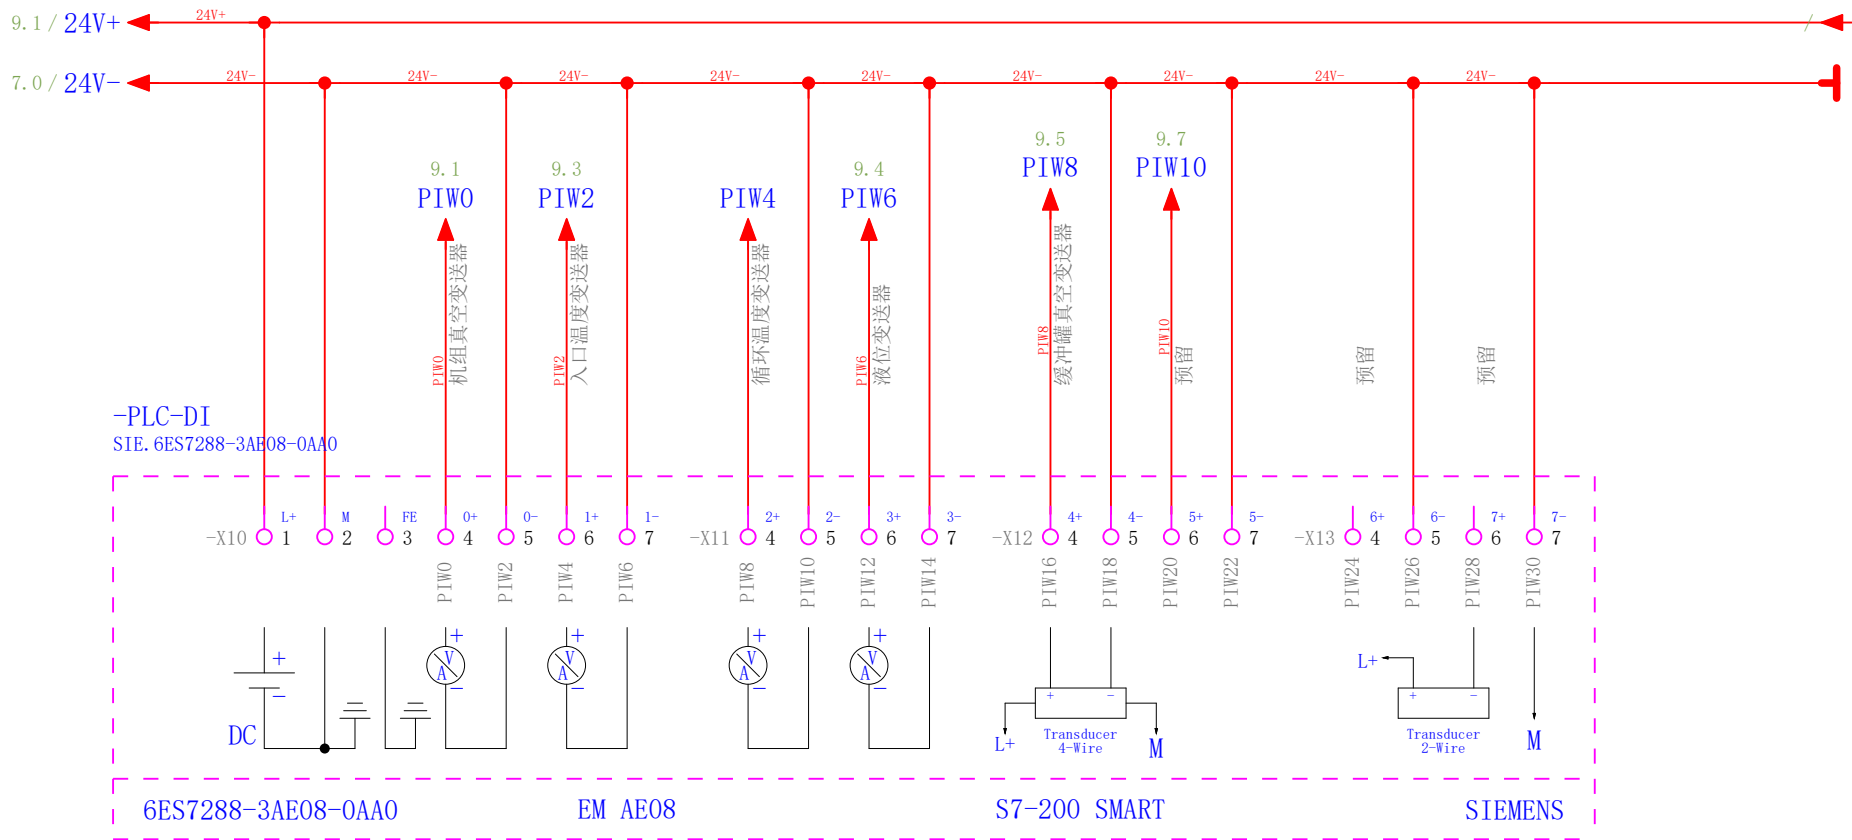


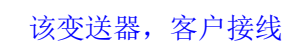


9
版权保护。严令禁止在未获得明确授权的情况下，转发和复制本文档，利用及传播其内容。

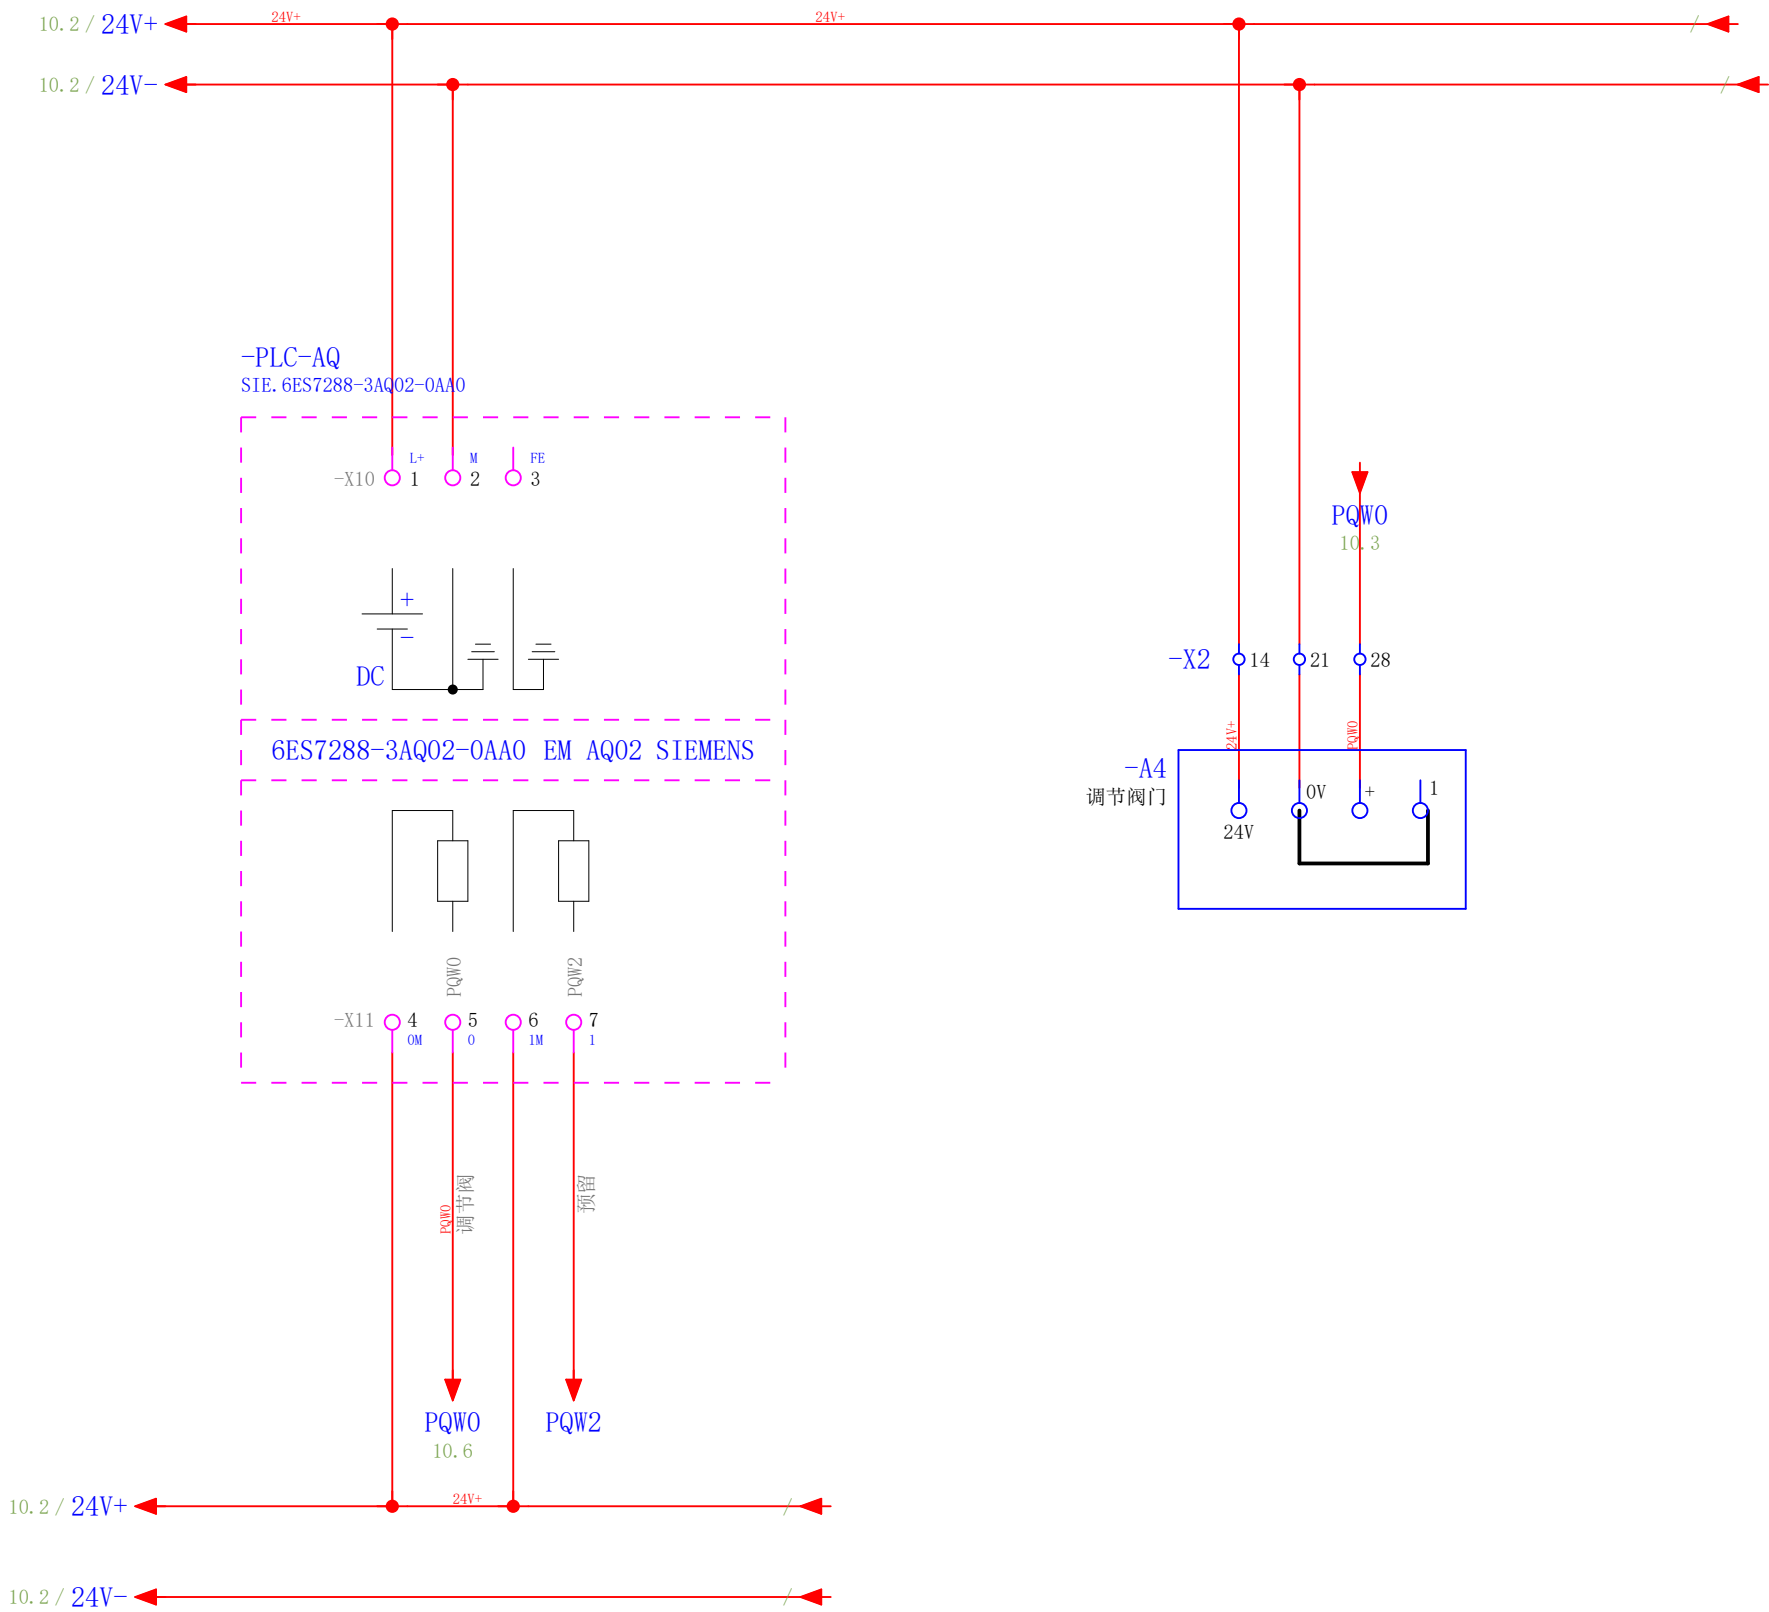


版权保护。严令禁止在未获得明确授权的情况下，转发和复制本文档，利用及传播其内容。


HMI

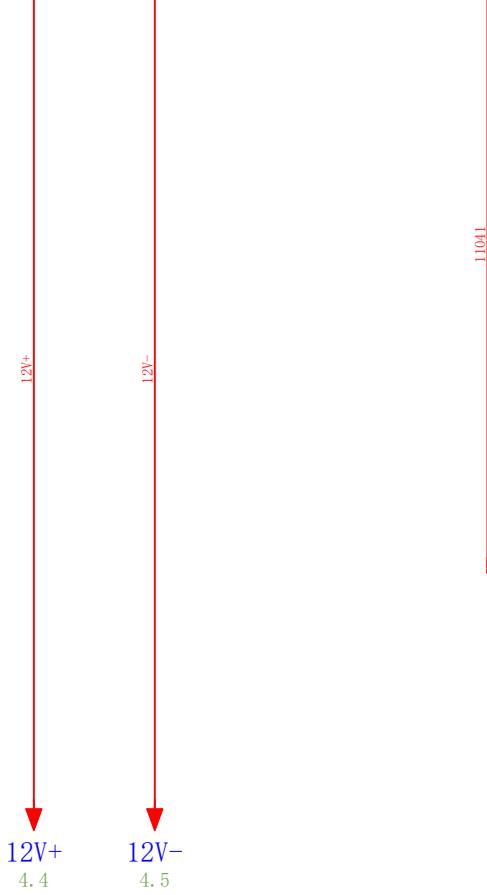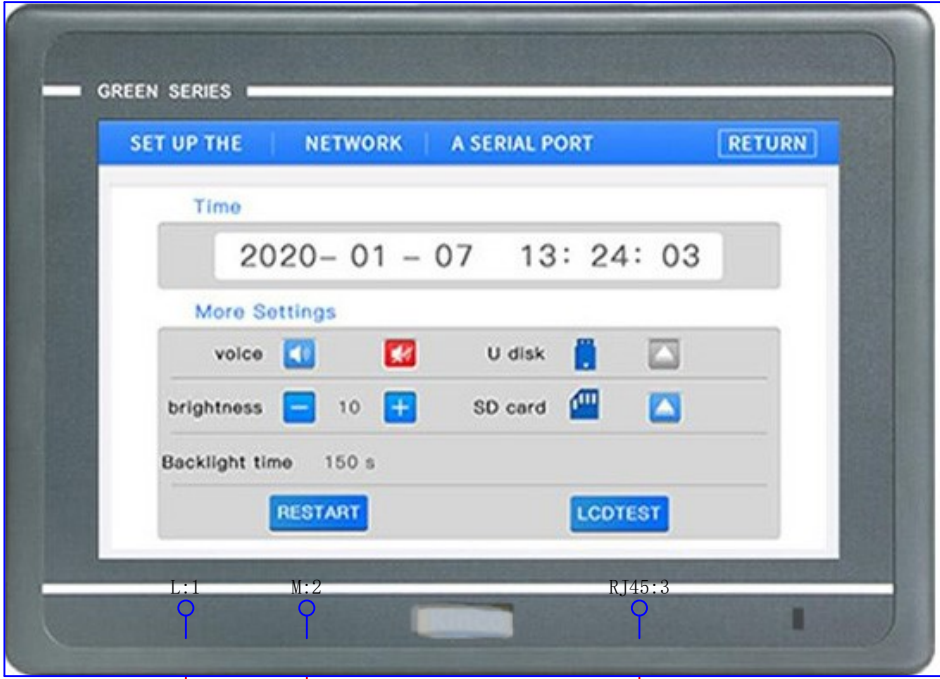

-A1

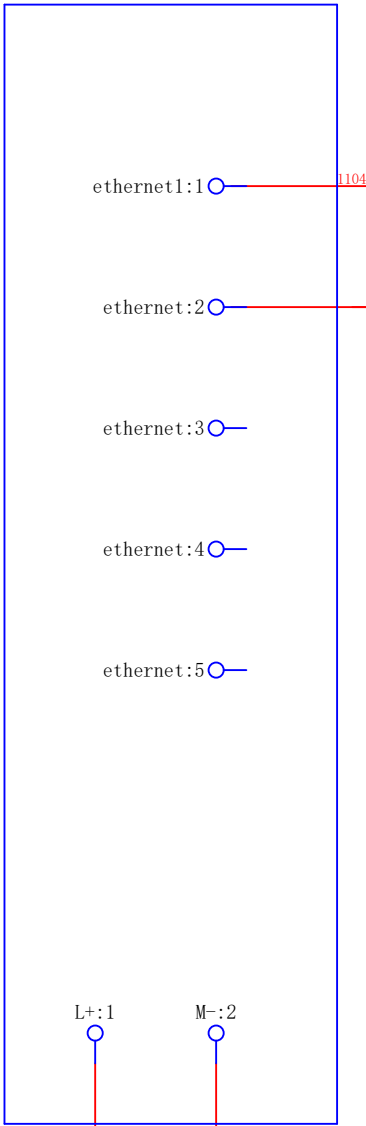

-PLC1

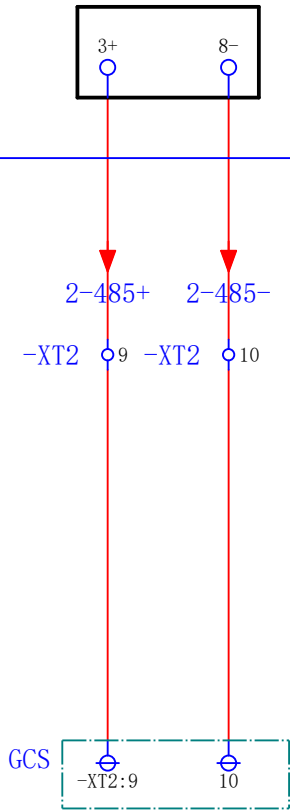

			项目名称2023-34-12014-1	项目编号2023-34-12014	冉昆真空科技有限公司	通讯界面		=	&EAA	
			X-10175KW液环罗茨机组	图号					页11	
修改	日期	姓名	创建者虎存山	批准人				+	页11从17	

0

1

2

3

4

5

6

7

8

9

PLC 地址概览

F48_001

CPU（间接的）	PLC 地址	数据类型	符号地址(自动)	功能文本(自动)	方向	规划对象名称
					未定义	
					未定义	
					未定义	
					未定义	
	I0.0	BOOL		复位	输入端	
	I0.1	BOOL		急停	输入端	
	I0.2	BOOL		启动	输入端	
	I0.3	BOOL		停止	输入端	
	I0.4	BOOL		手自动切换	输入端	
	I0.5	BOOL		流量开关	输入端	
	I0.6	BOOL		罗茨泵过载	输入端	
	I0.7	BOOL		软起故障	输入端	
	I1.0	BOOL		本地/DCS	输入端	
	I1.1	BOOL		预留	输入端	
	I1.2	BOOL		=	输入端	
	I1.3	BOOL		=	输入端	
	I1.4	BOOL		=	输入端	
	I1.5	BOOL		=	输入端	
	I1.6	BOOL		=	输入端	
	I1.7	BOOL		=	输入端	
	I2.0	BOOL		=	输入端	
	I2.1	BOOL		=	输入端	
	I2.2	BOOL		=	输入端	
	I2.3	BOOL		=	输入端	
	I2.4	BOOL		=	输入端	
	I2.5	BOOL		=	输入端	
	I2.6	BOOL		=	输入端	

版
权
保
护
。
严
令
禁
止
在
未
获
得
明
确
授
权
的
情
况
下
转
发
和
复
制
本
文
档
，
利
用
及
传
播
其
内
容
。

&EAA/11

1. a

			项目名称2023-34-12014-1	项目编号2023-34-12014	冉昆真空科技有限公司			=	&EAB
			X-10175KW液环罗茨机组	图号					
修改	日期	姓名	创建者虎存山	批准人		日期2024/1/15	校对虎存山		页1
									页数12 从17

版权保护。严令禁止在未获得明确授权的情况下，转发和复制本文档，利用及传播其内容。

0	1	2	3	4	5	6	7	8	9
PLC 地址概览									F48_001
CPU（间接的）		PLC 地址	数据类型	符号地址(自动)	功能文本(自动)	方向	规划对象名称		
		Q1. 0	BOOL		补液阀	输出端			
		Q1. 1	BOOL		排污阀	输出端			
		Q1. 2	BOOL		预留	输出端			
		Q1. 3	BOOL		=	输出端			
		Q1. 4	BOOL		=	输出端			
		Q1. 5	BOOL		=	输出端			
		Q1. 6	BOOL		=	输出端			
		Q1. 7	BOOL		=	输出端			
1. a									2
			项目名称 2023-34-12014-1	项目编号 2023-34-12014	冉昆真空科技有限公司 		=	&EAB	
			X-101 75KW液环罗茨机组	图号					
							+	页 1. b	
修改	日期	姓名	创建者 虎存山	批准人		日期 2024/1/15	校对 虎存山		页数 14 从 17

版权保护。严令禁止在未获得明确授权的情况下转发和复制本文档，利用及传播其内容。

版权所有。严禁禁止在未获得明确授权的情况下，转发和复制本文档，利用及传播其内容。

