



版权保护。严禁禁止在未获得明确授权的情况下，转发和复制本文档，利用及传播其内容。

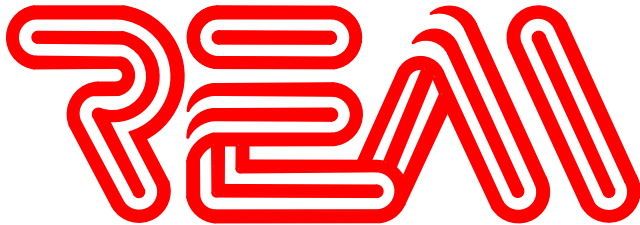

EPLAN GmbH & Co. KG


An der alten Ziegelei 2
40789 Monheim am Rhein
电话 +49 (0)2173 - 39 64 - 0

公司/客户	
项目描述	GCS固定柜
项目编号	2023-34-12014
代理	EPLAN
制造商(公司)	EPLAN GmbH & Co. KG
路径	EPLAN 示例项目
项目名称	2023-34-12014
制作	
类型	
安装地点	
项目负责人	
部件特点	
创建日期	2024/1/12
编辑日期	2024/1/13
	源自(缩写) 虎存山
	页数 14

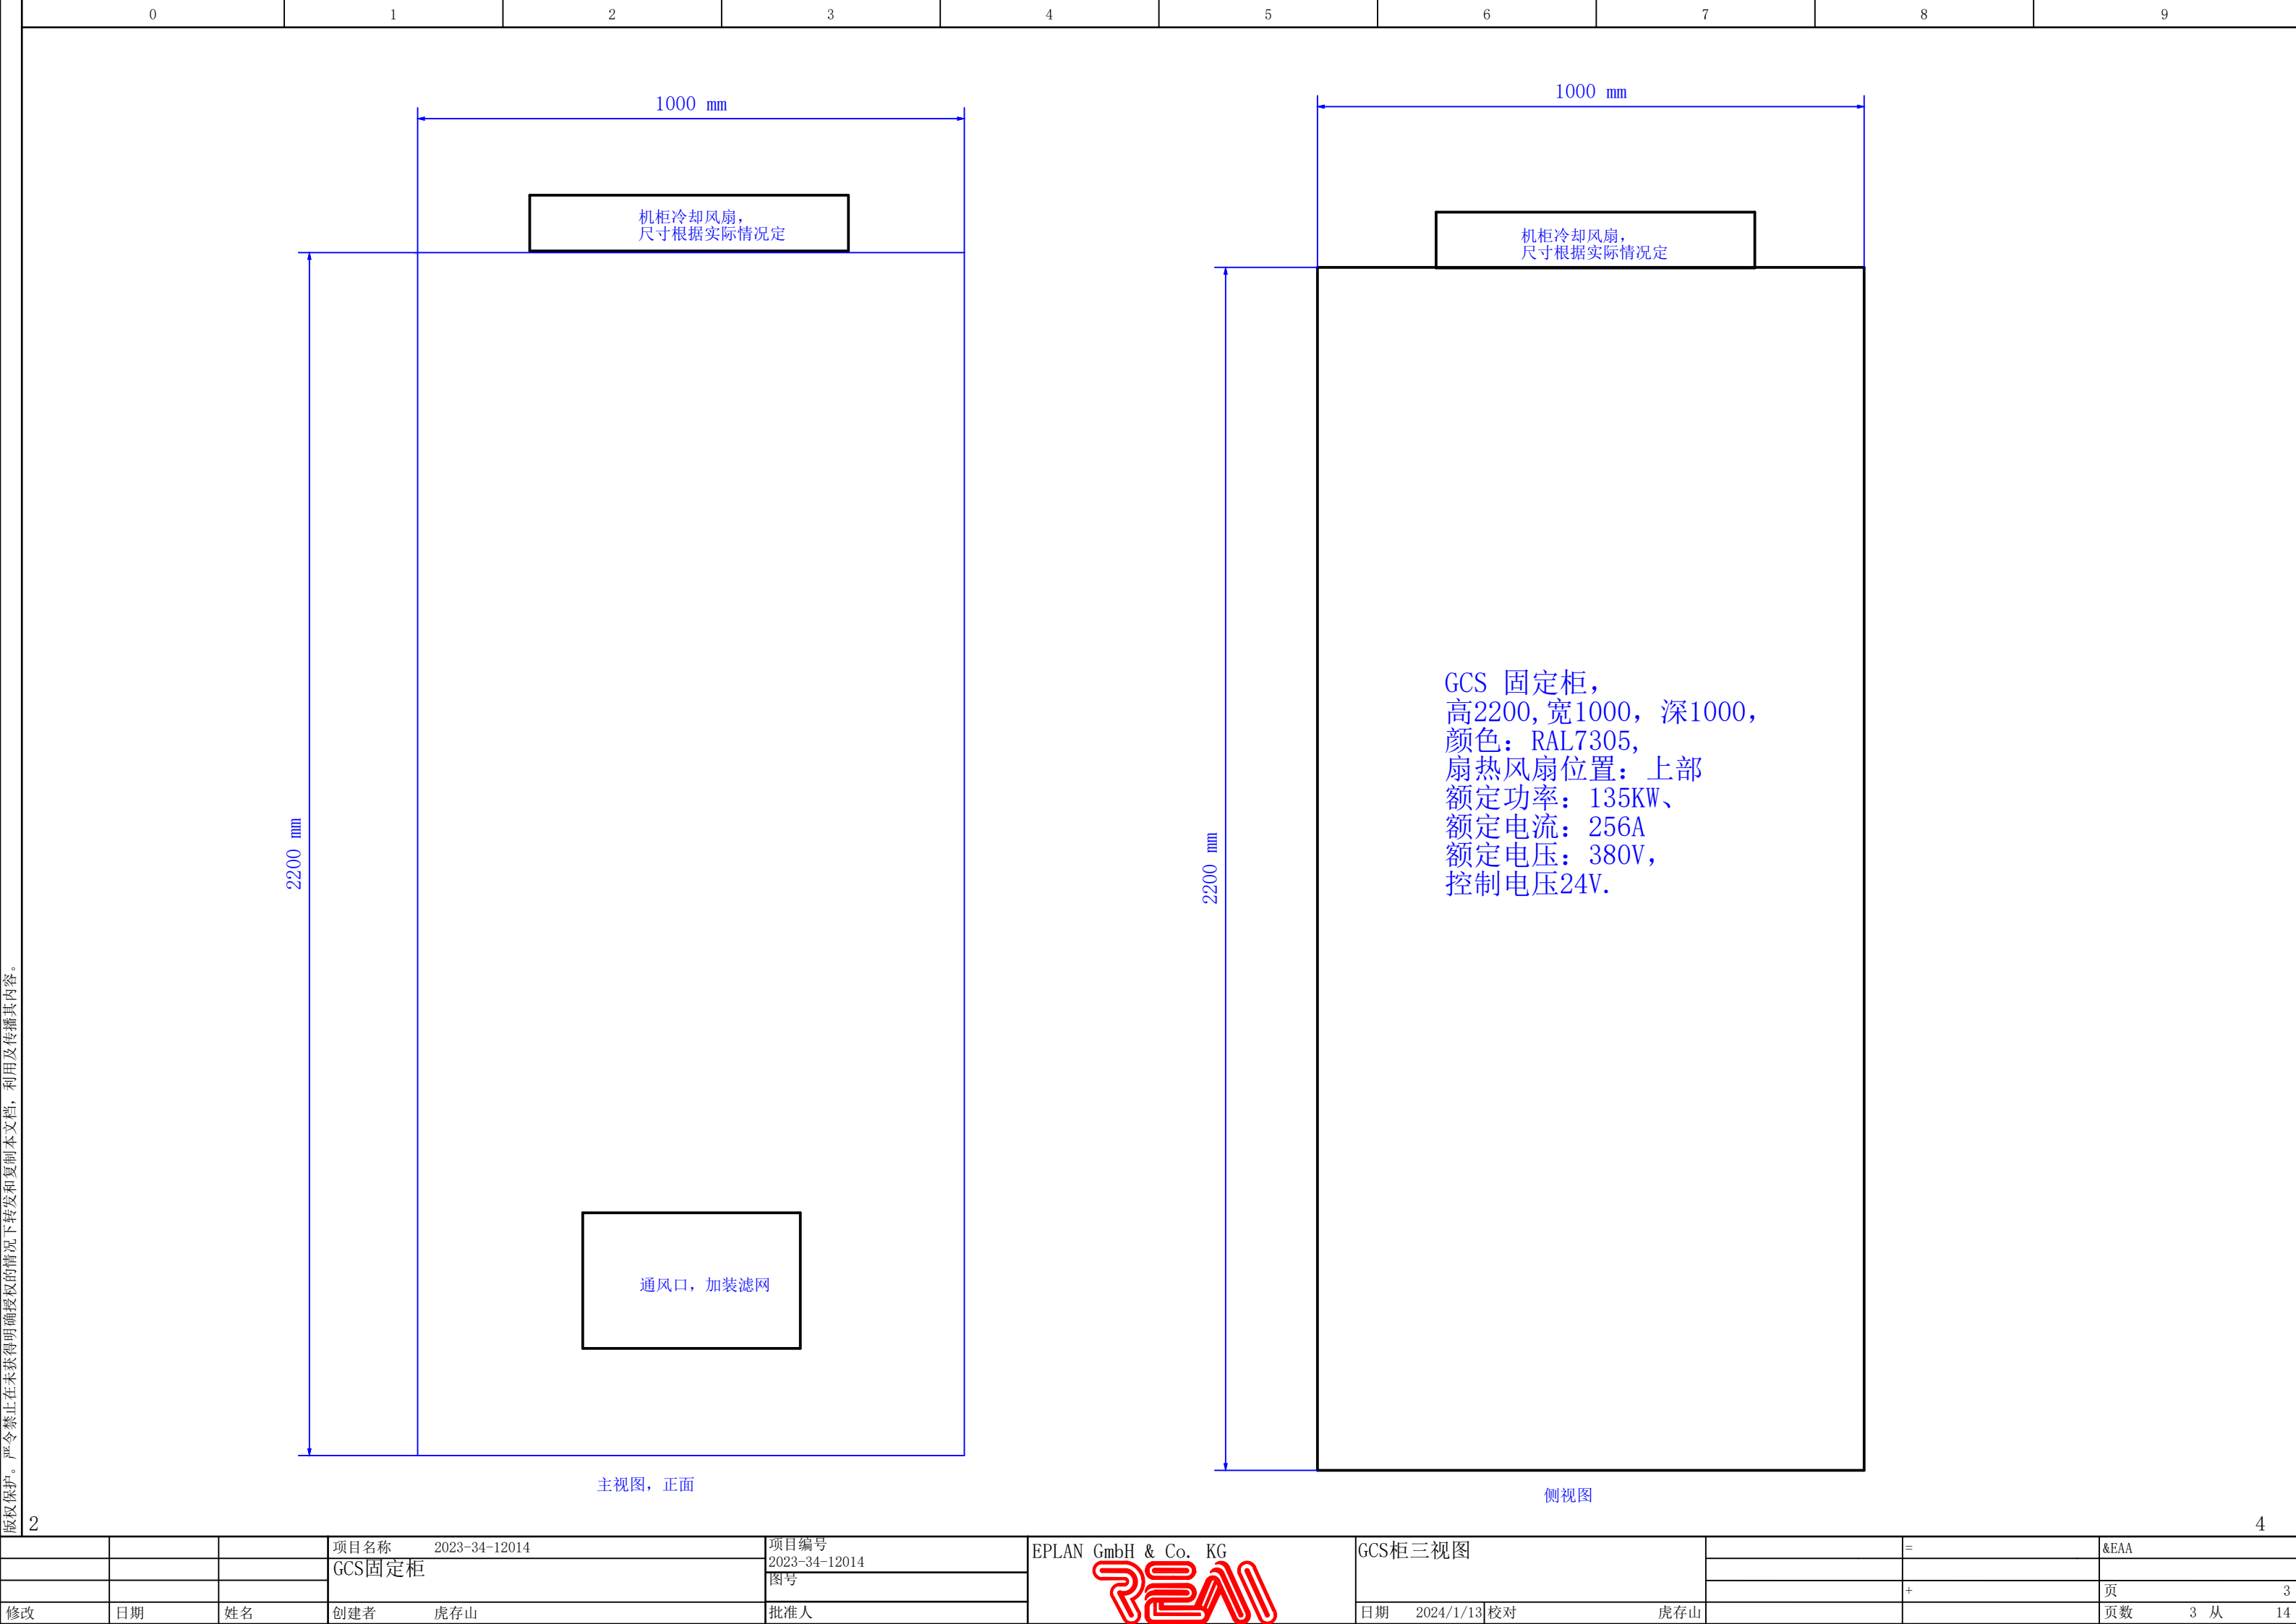


版权保护。严令禁止在未获得明确授权的情况下，转发和复制本文档，利用及传播其内容。


			项目名称 2023-34-12014	项目编号 2023-34-12014	EPLAN GmbH & Co. KG 	GCS柜三视图		=	&EAA	
			GCS固定柜	图号						
								+	页 3	
修改	日期	姓名	创建者 虎存山	批准人			日期 2024/1/13 校对 虎存山		页数 3 从	14

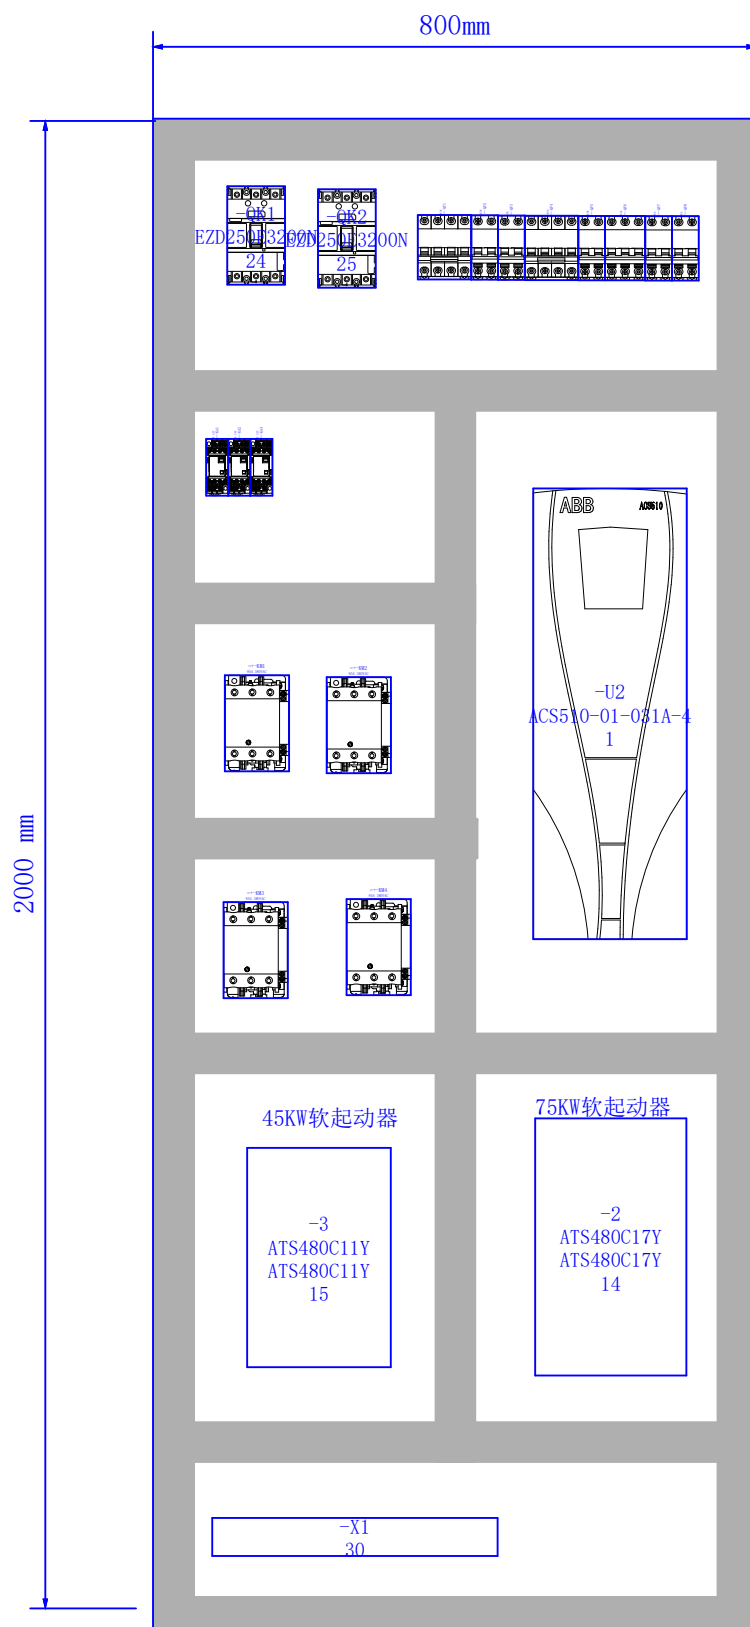


箱柜设备清单


序号	设备标识符	型号	规格
1	U2	ACS510-01-031A-4	15KW
2	QK1	EZD250E3200N	200A
3	QK2	EZD250E3200N	200A
4	QF1	SE. A9F19440	D40A
5	QF2	SE. A9F19220	D20A
6	QF3	SE. A9F19440	D40A
7	QF4	SE. A9F19220	D20A
8	QF5	SE. A9F19210	D10A
9	KM1	SE. LC1D95Q7C	95A 380VAC
10	KM2	SE. LC1D95Q7C	95A 380VAC
11	KM3	SE. LC1D95Q7C	95A 380VAC
12	KM4	SE. LC1D95Q7C	95A 380VAC
13	2	ATS480C17Y	
14	3	ATS480C11Y	

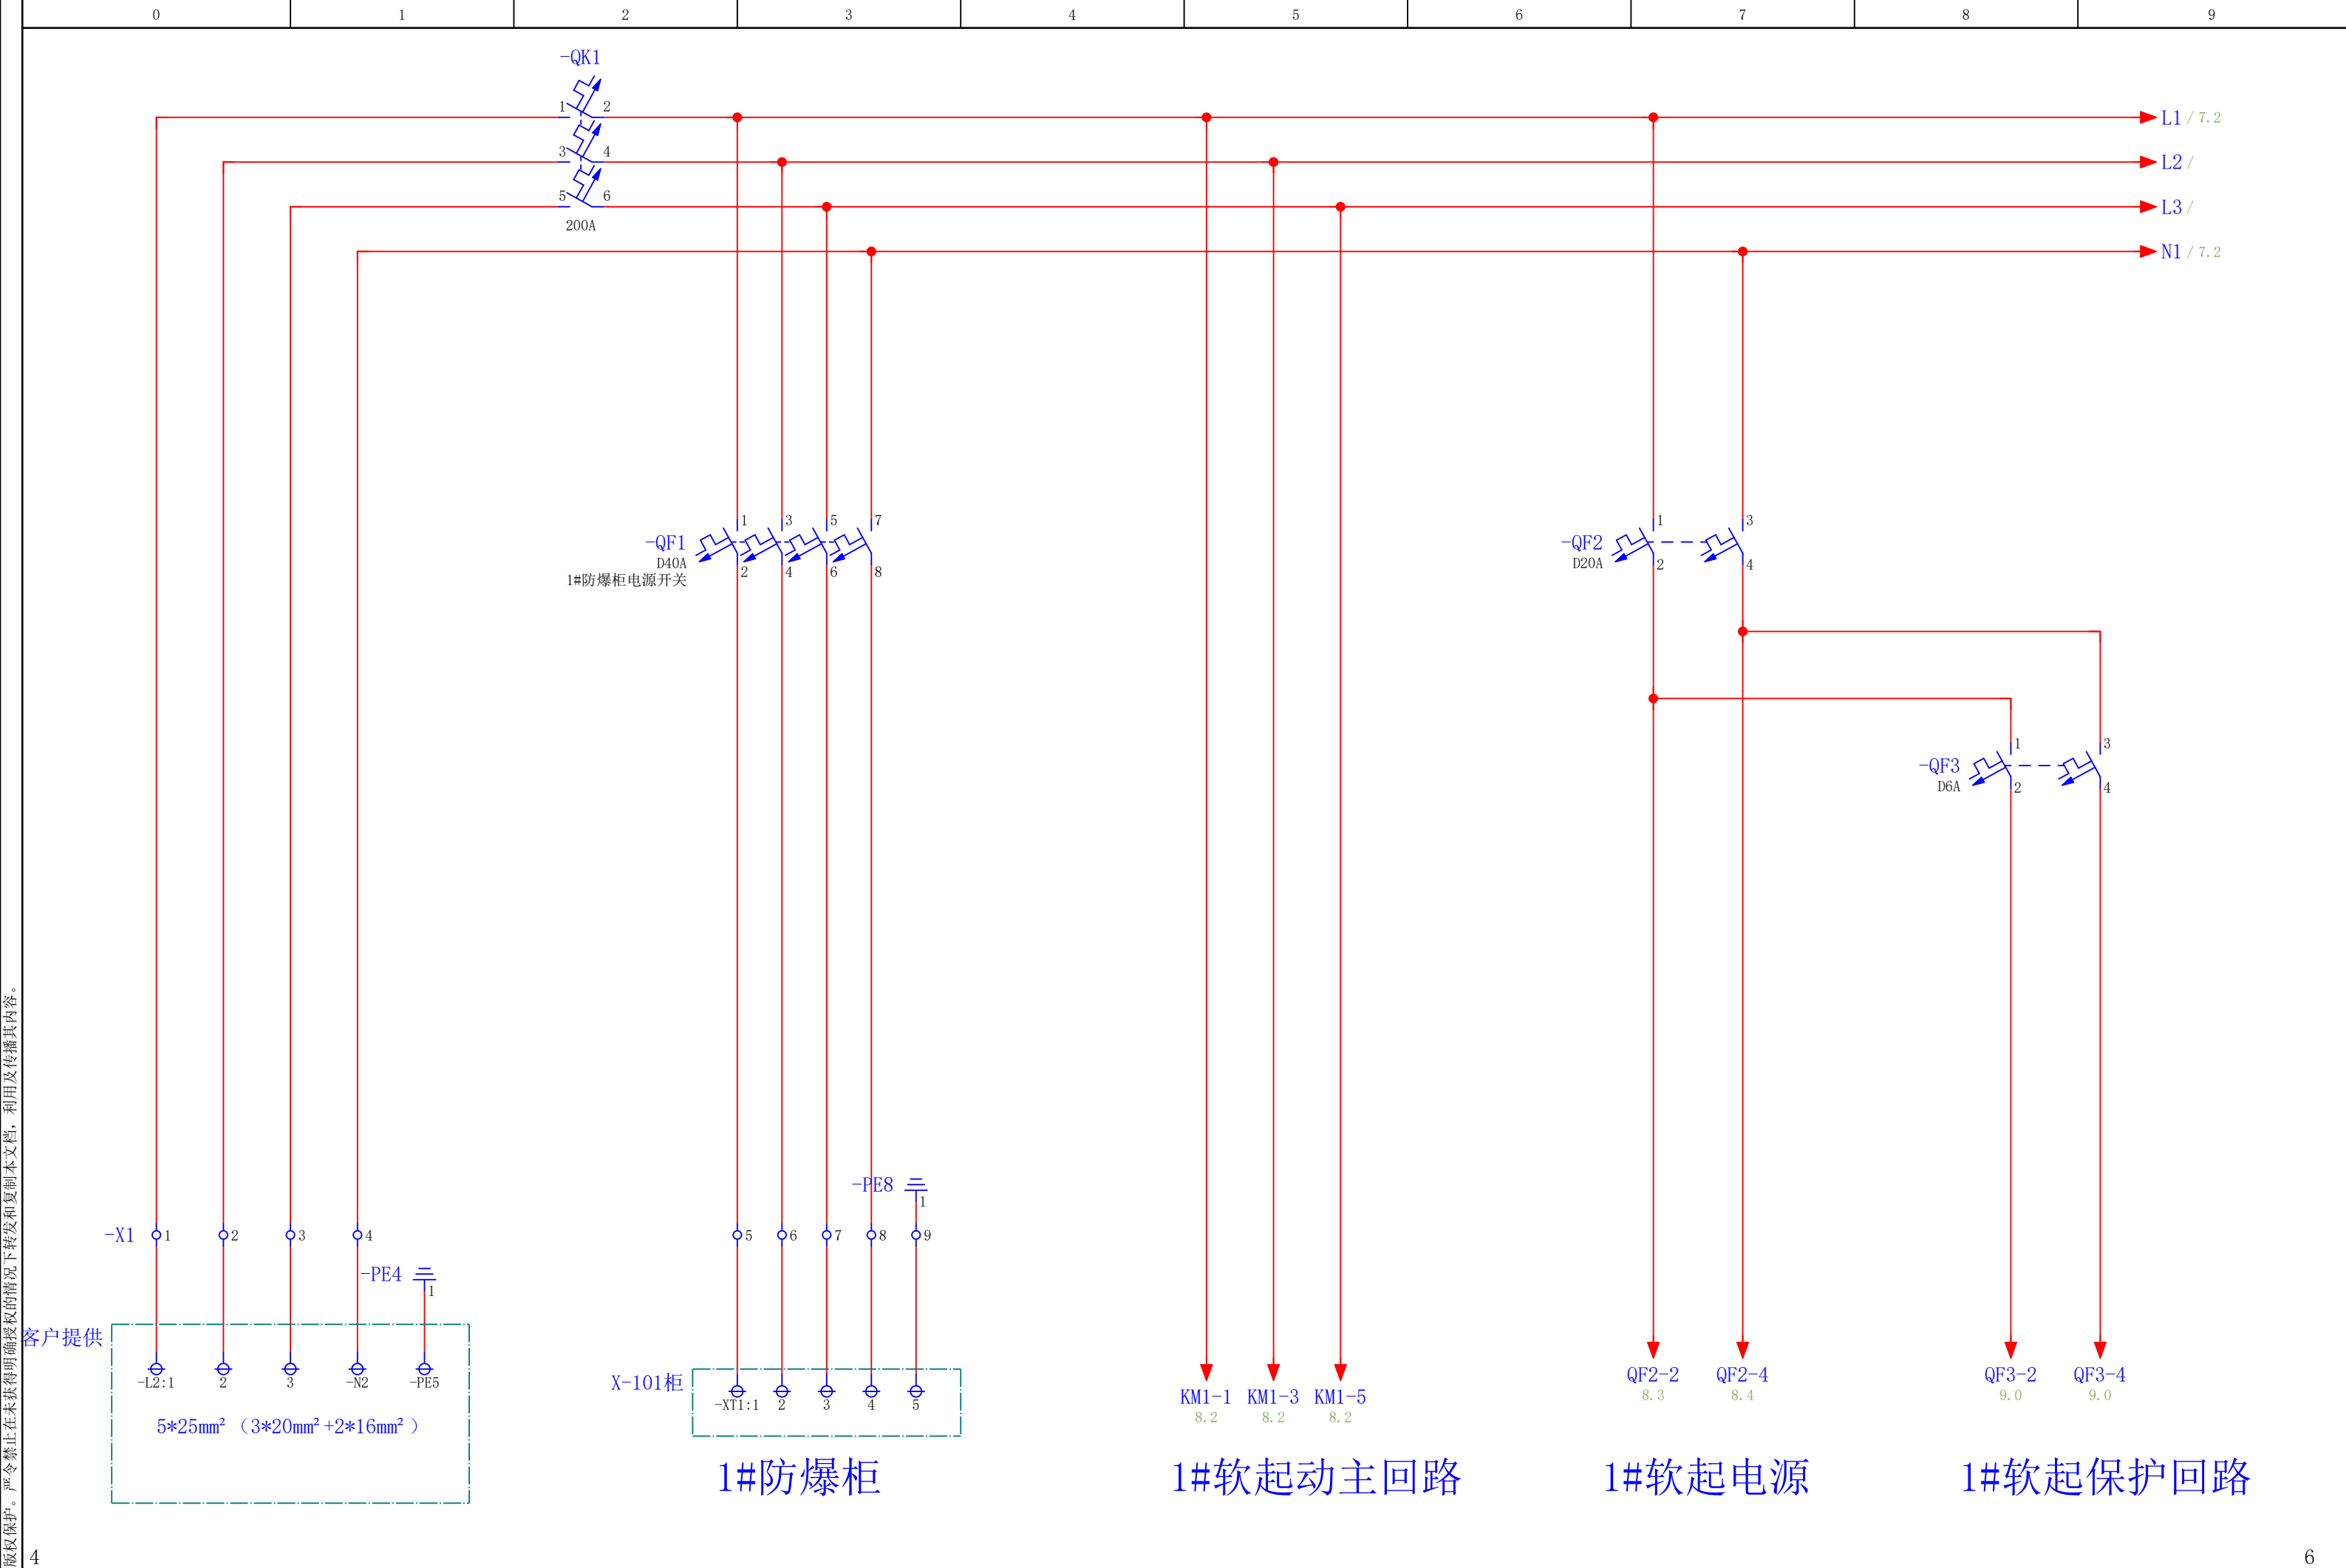

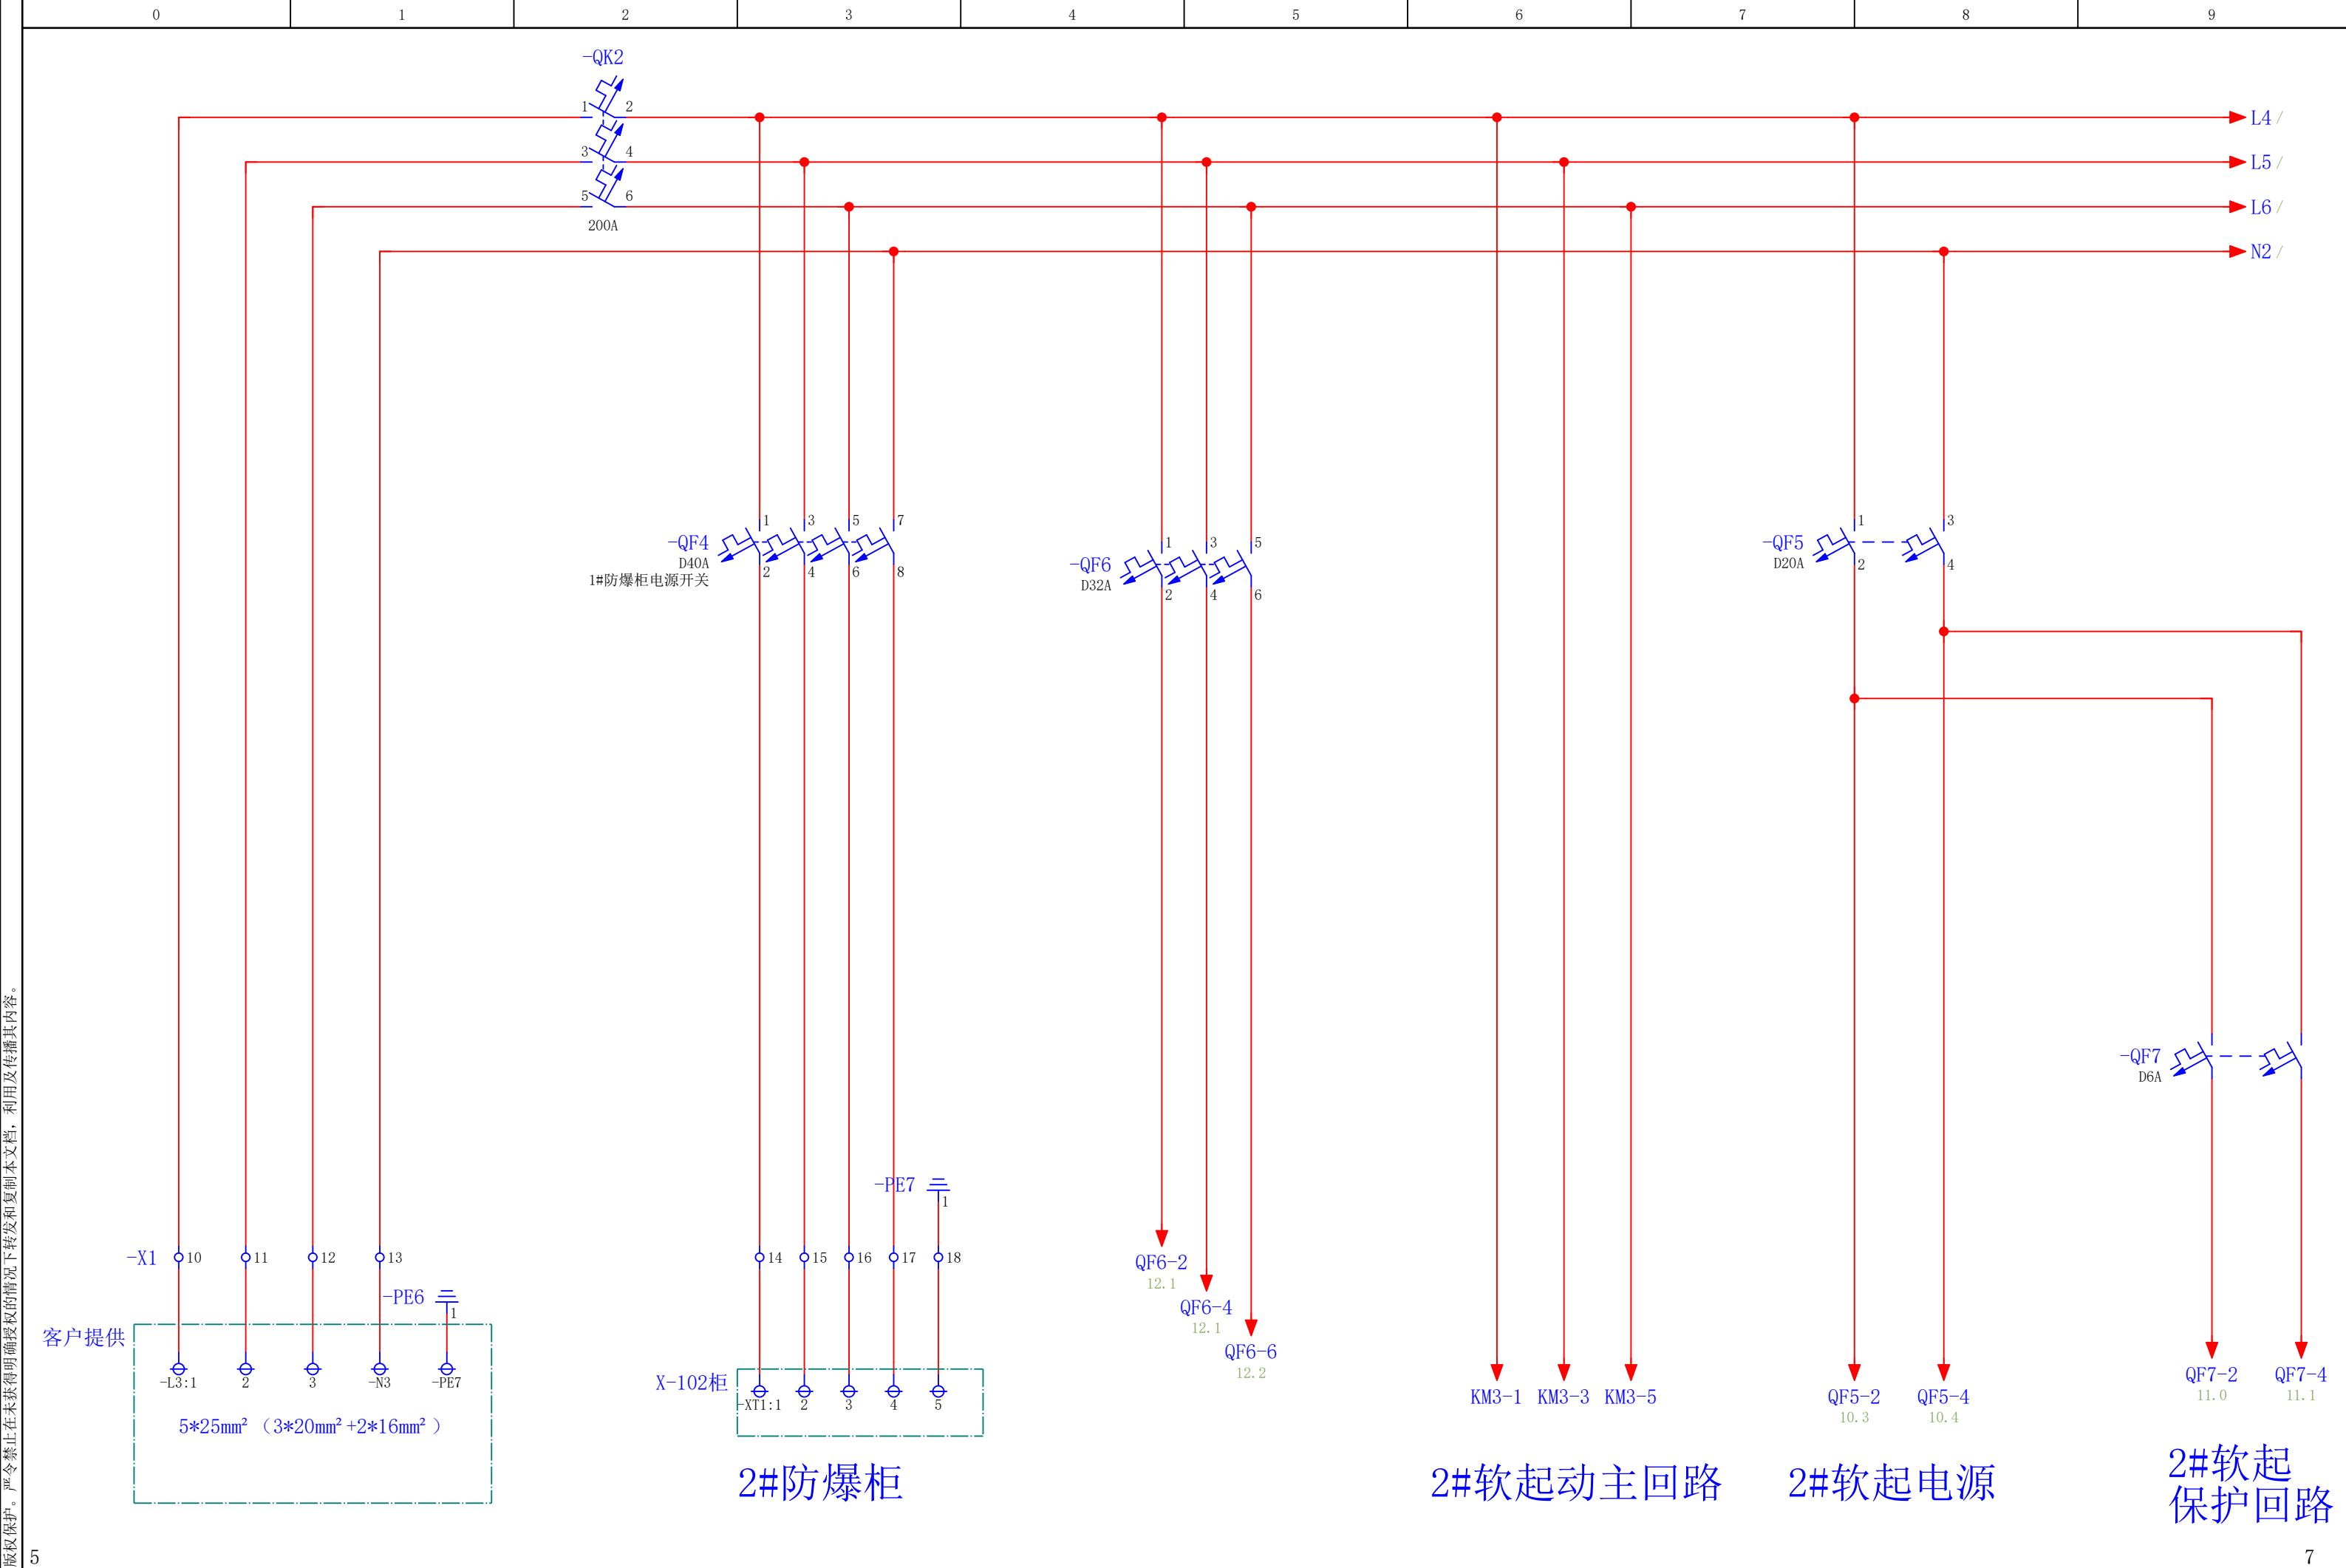

版权保护。严禁禁止在未获得明确授权的情况下转发和复制本文档，利用及传播其内容。

 
			项目名称	2023-34-12014	项目编号	EPLAN GmbH & Co. KG	X-102 (45KW) 主回路			=	&EAA	
			GCS固定柜		2023-34-12014							
					图号					+	页	6
修改	日期	姓名	创建者	虎存山	批准人		日期	2024/1/13	校对	虎存山	页数	6 从 14

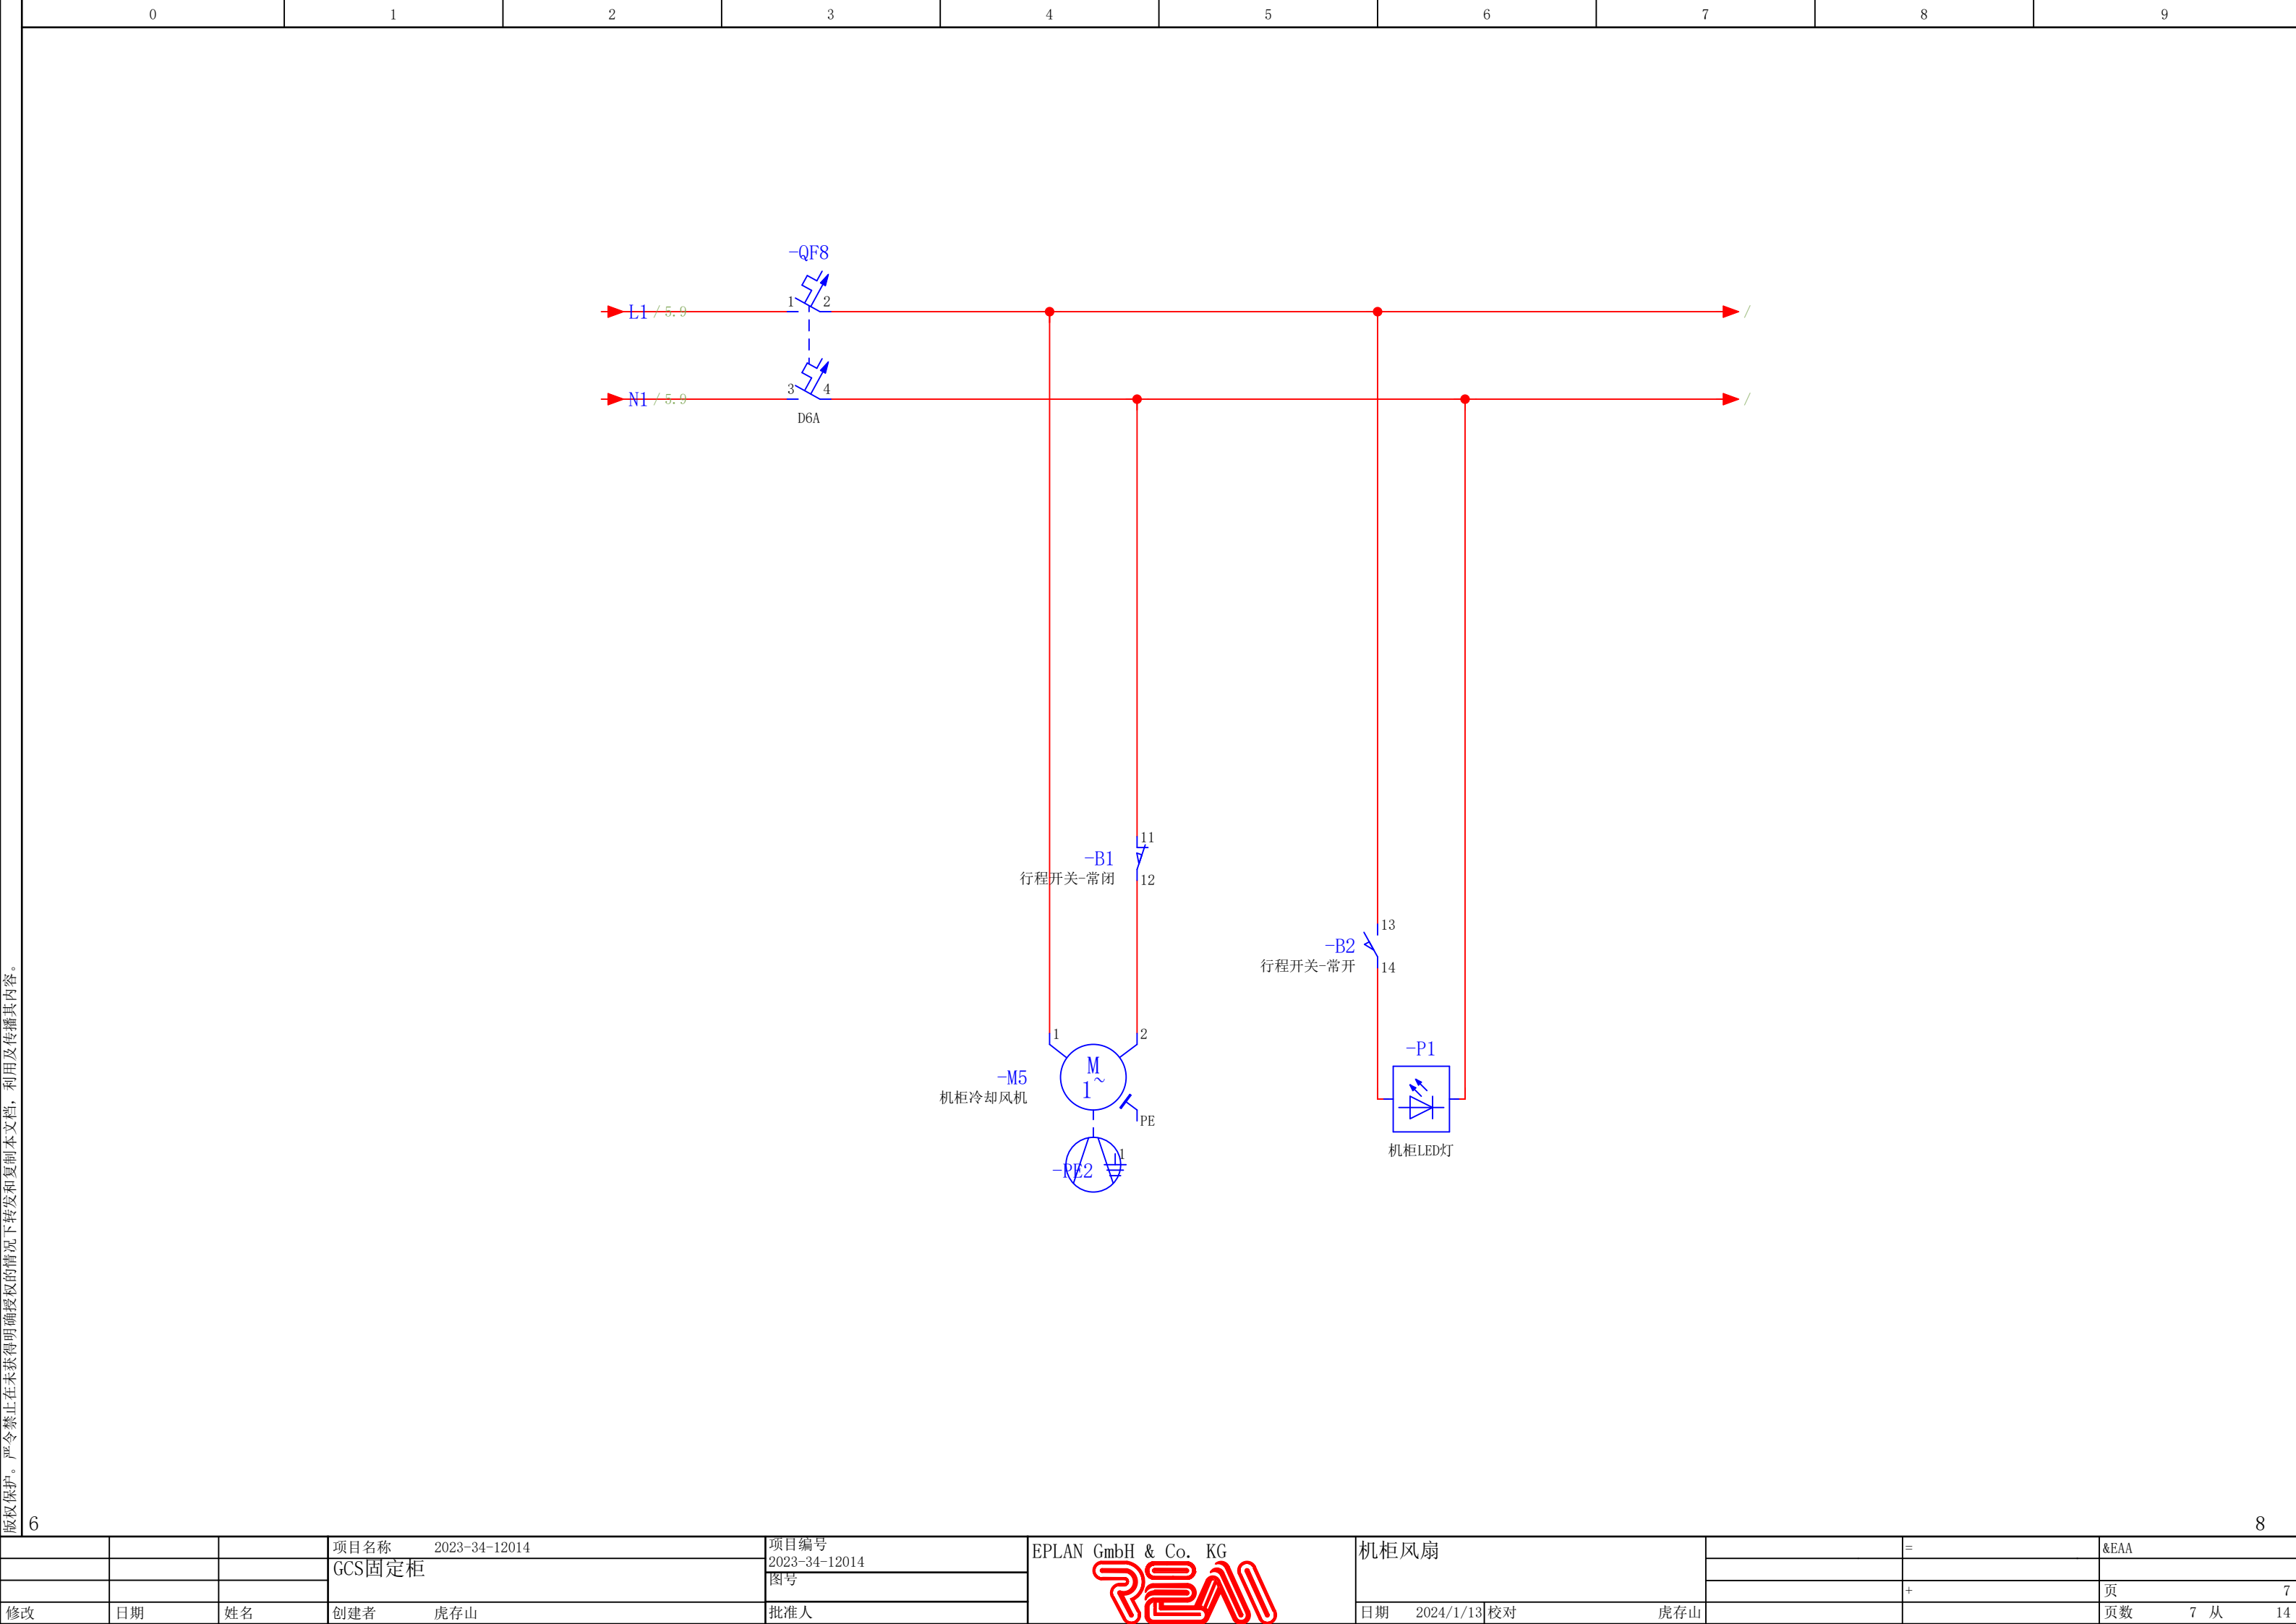


6
版权所有。严令禁止在未获得明确授权的情况下转发和复制本文档，利用及传播其内容。




			项目名称 2023-34-12014	项目编号 2023-34-12014	EPLAN GmbH & Co. KG 	X-101软起动机			=	&EAA	
			GCS固定柜	图号							
									+		8
修改	日期	姓名	创建者 虎存山	批准人		日期 2024/1/13	校对 虎存山			页数 8 从 14	

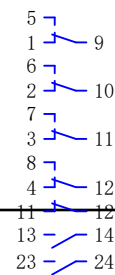

版权保护。严令禁止在未获得明确授权的情况下转发和复制本文档，利用及传播其内容。

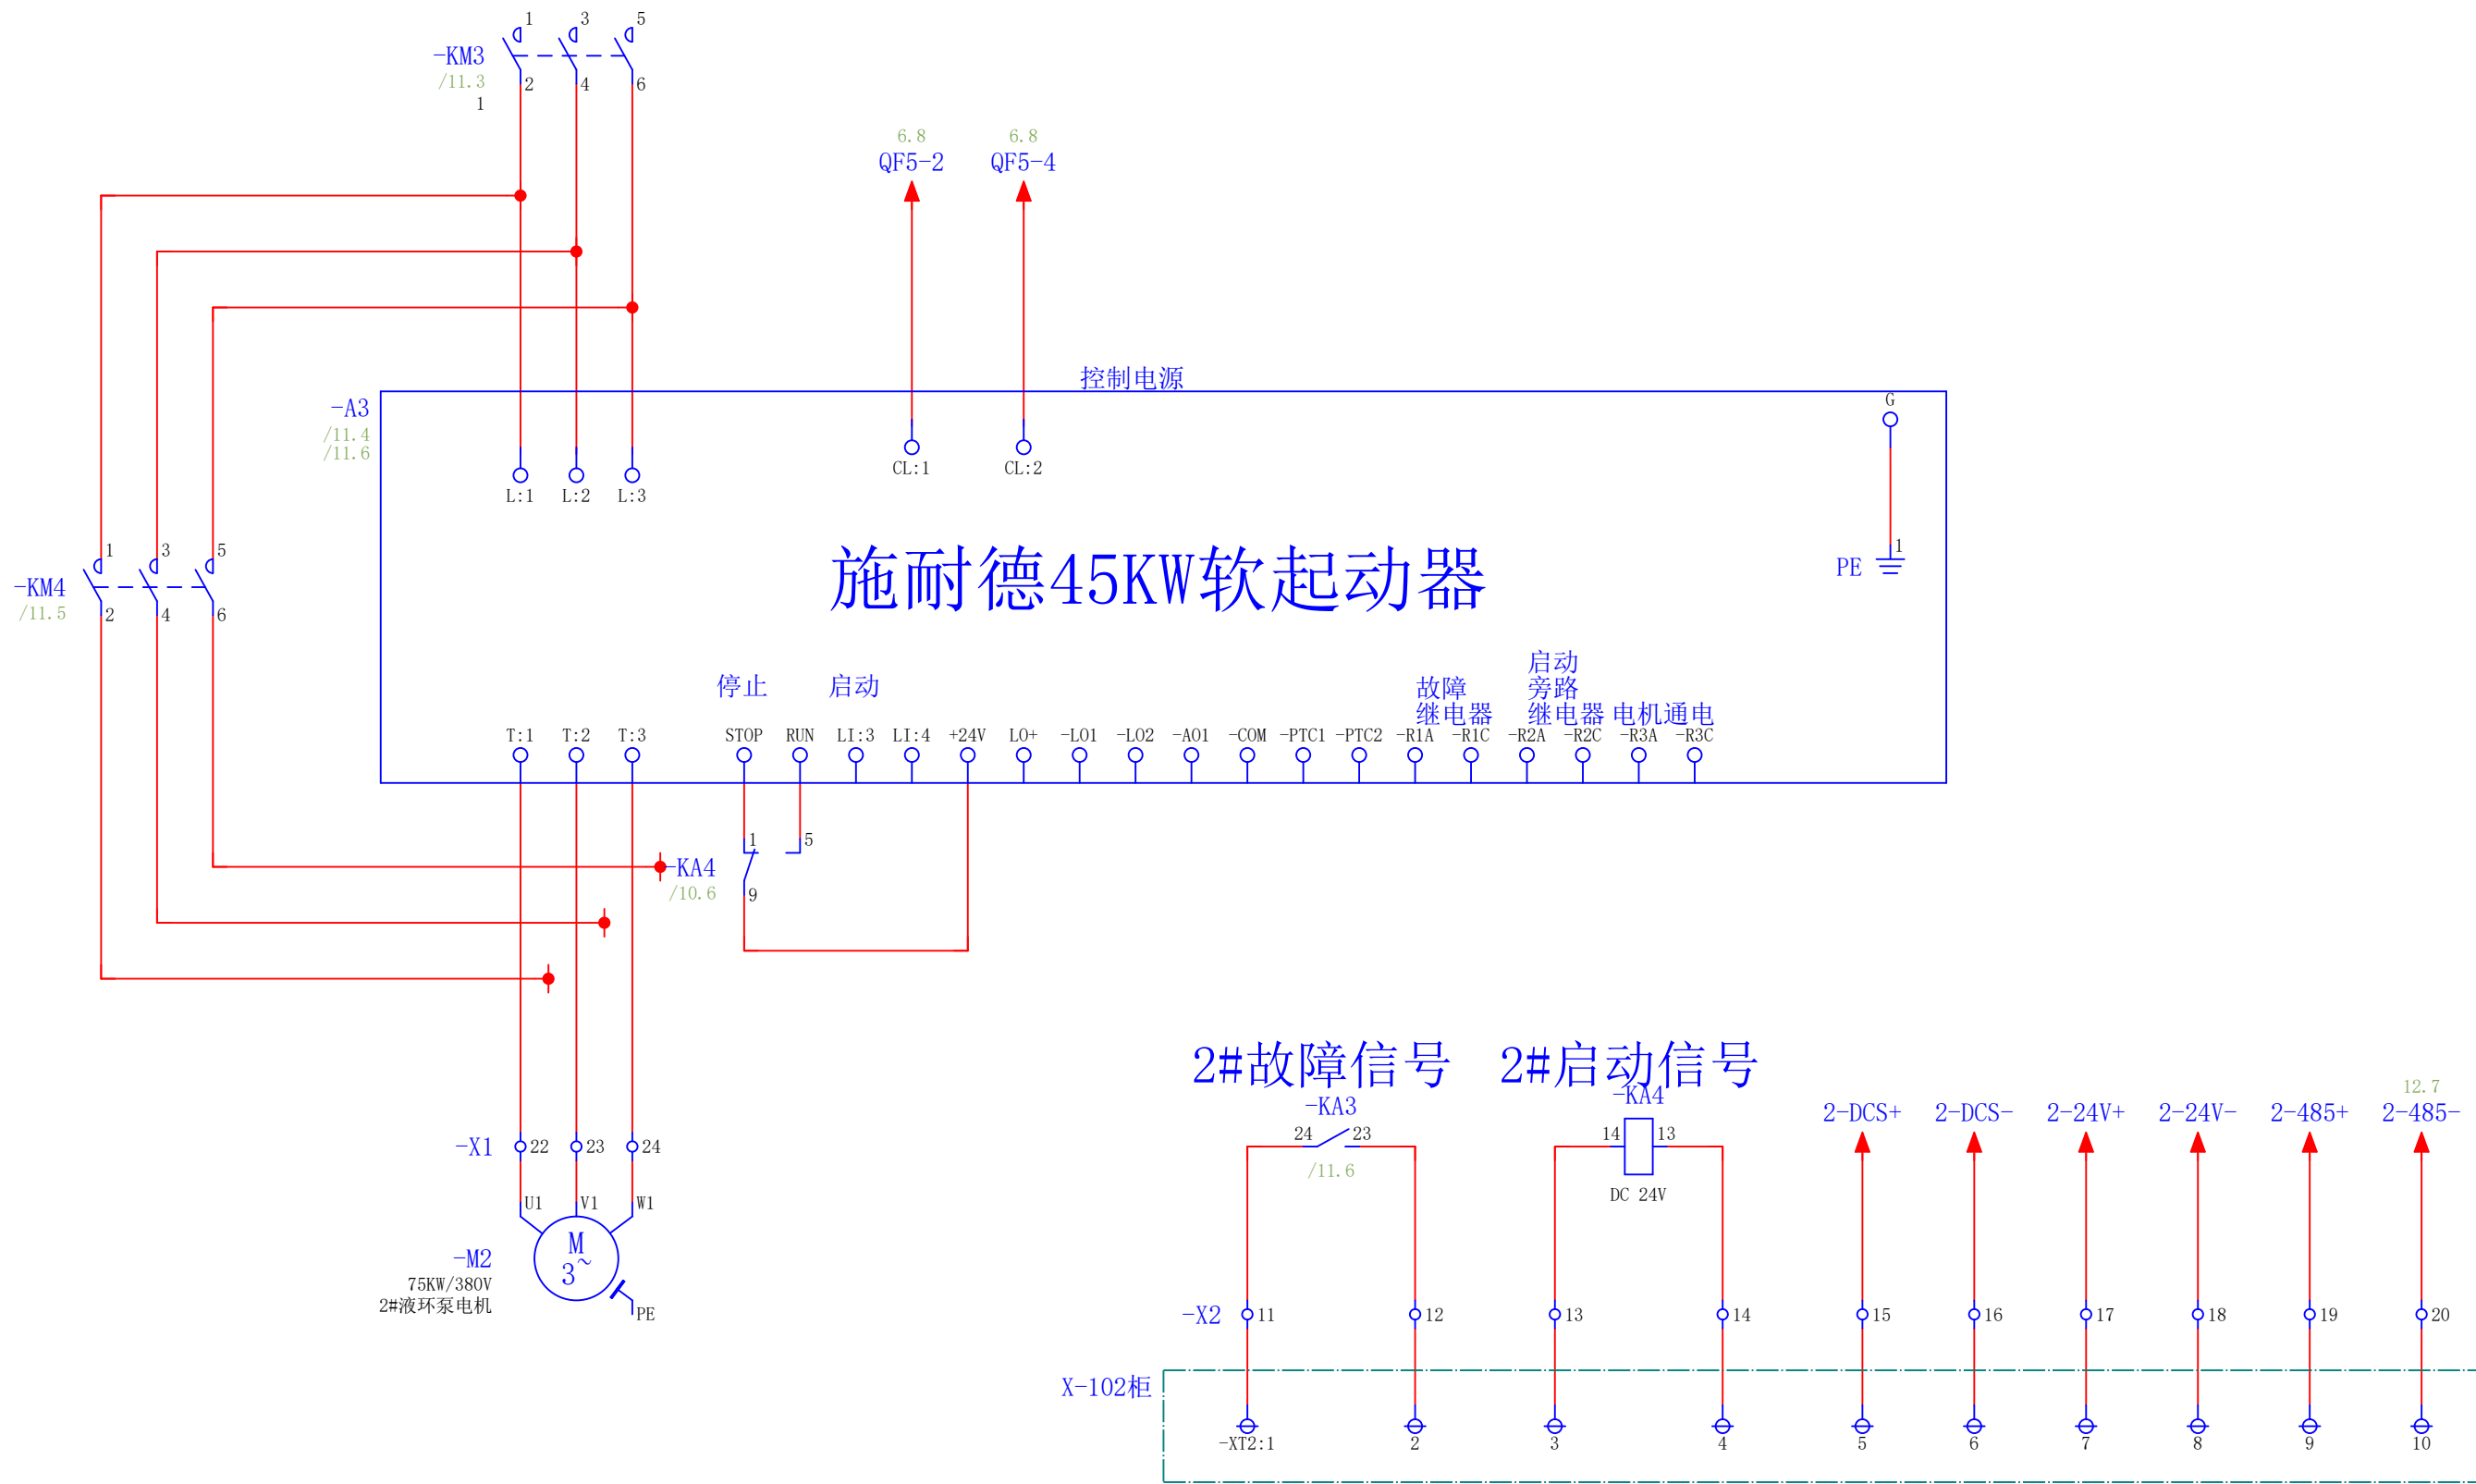



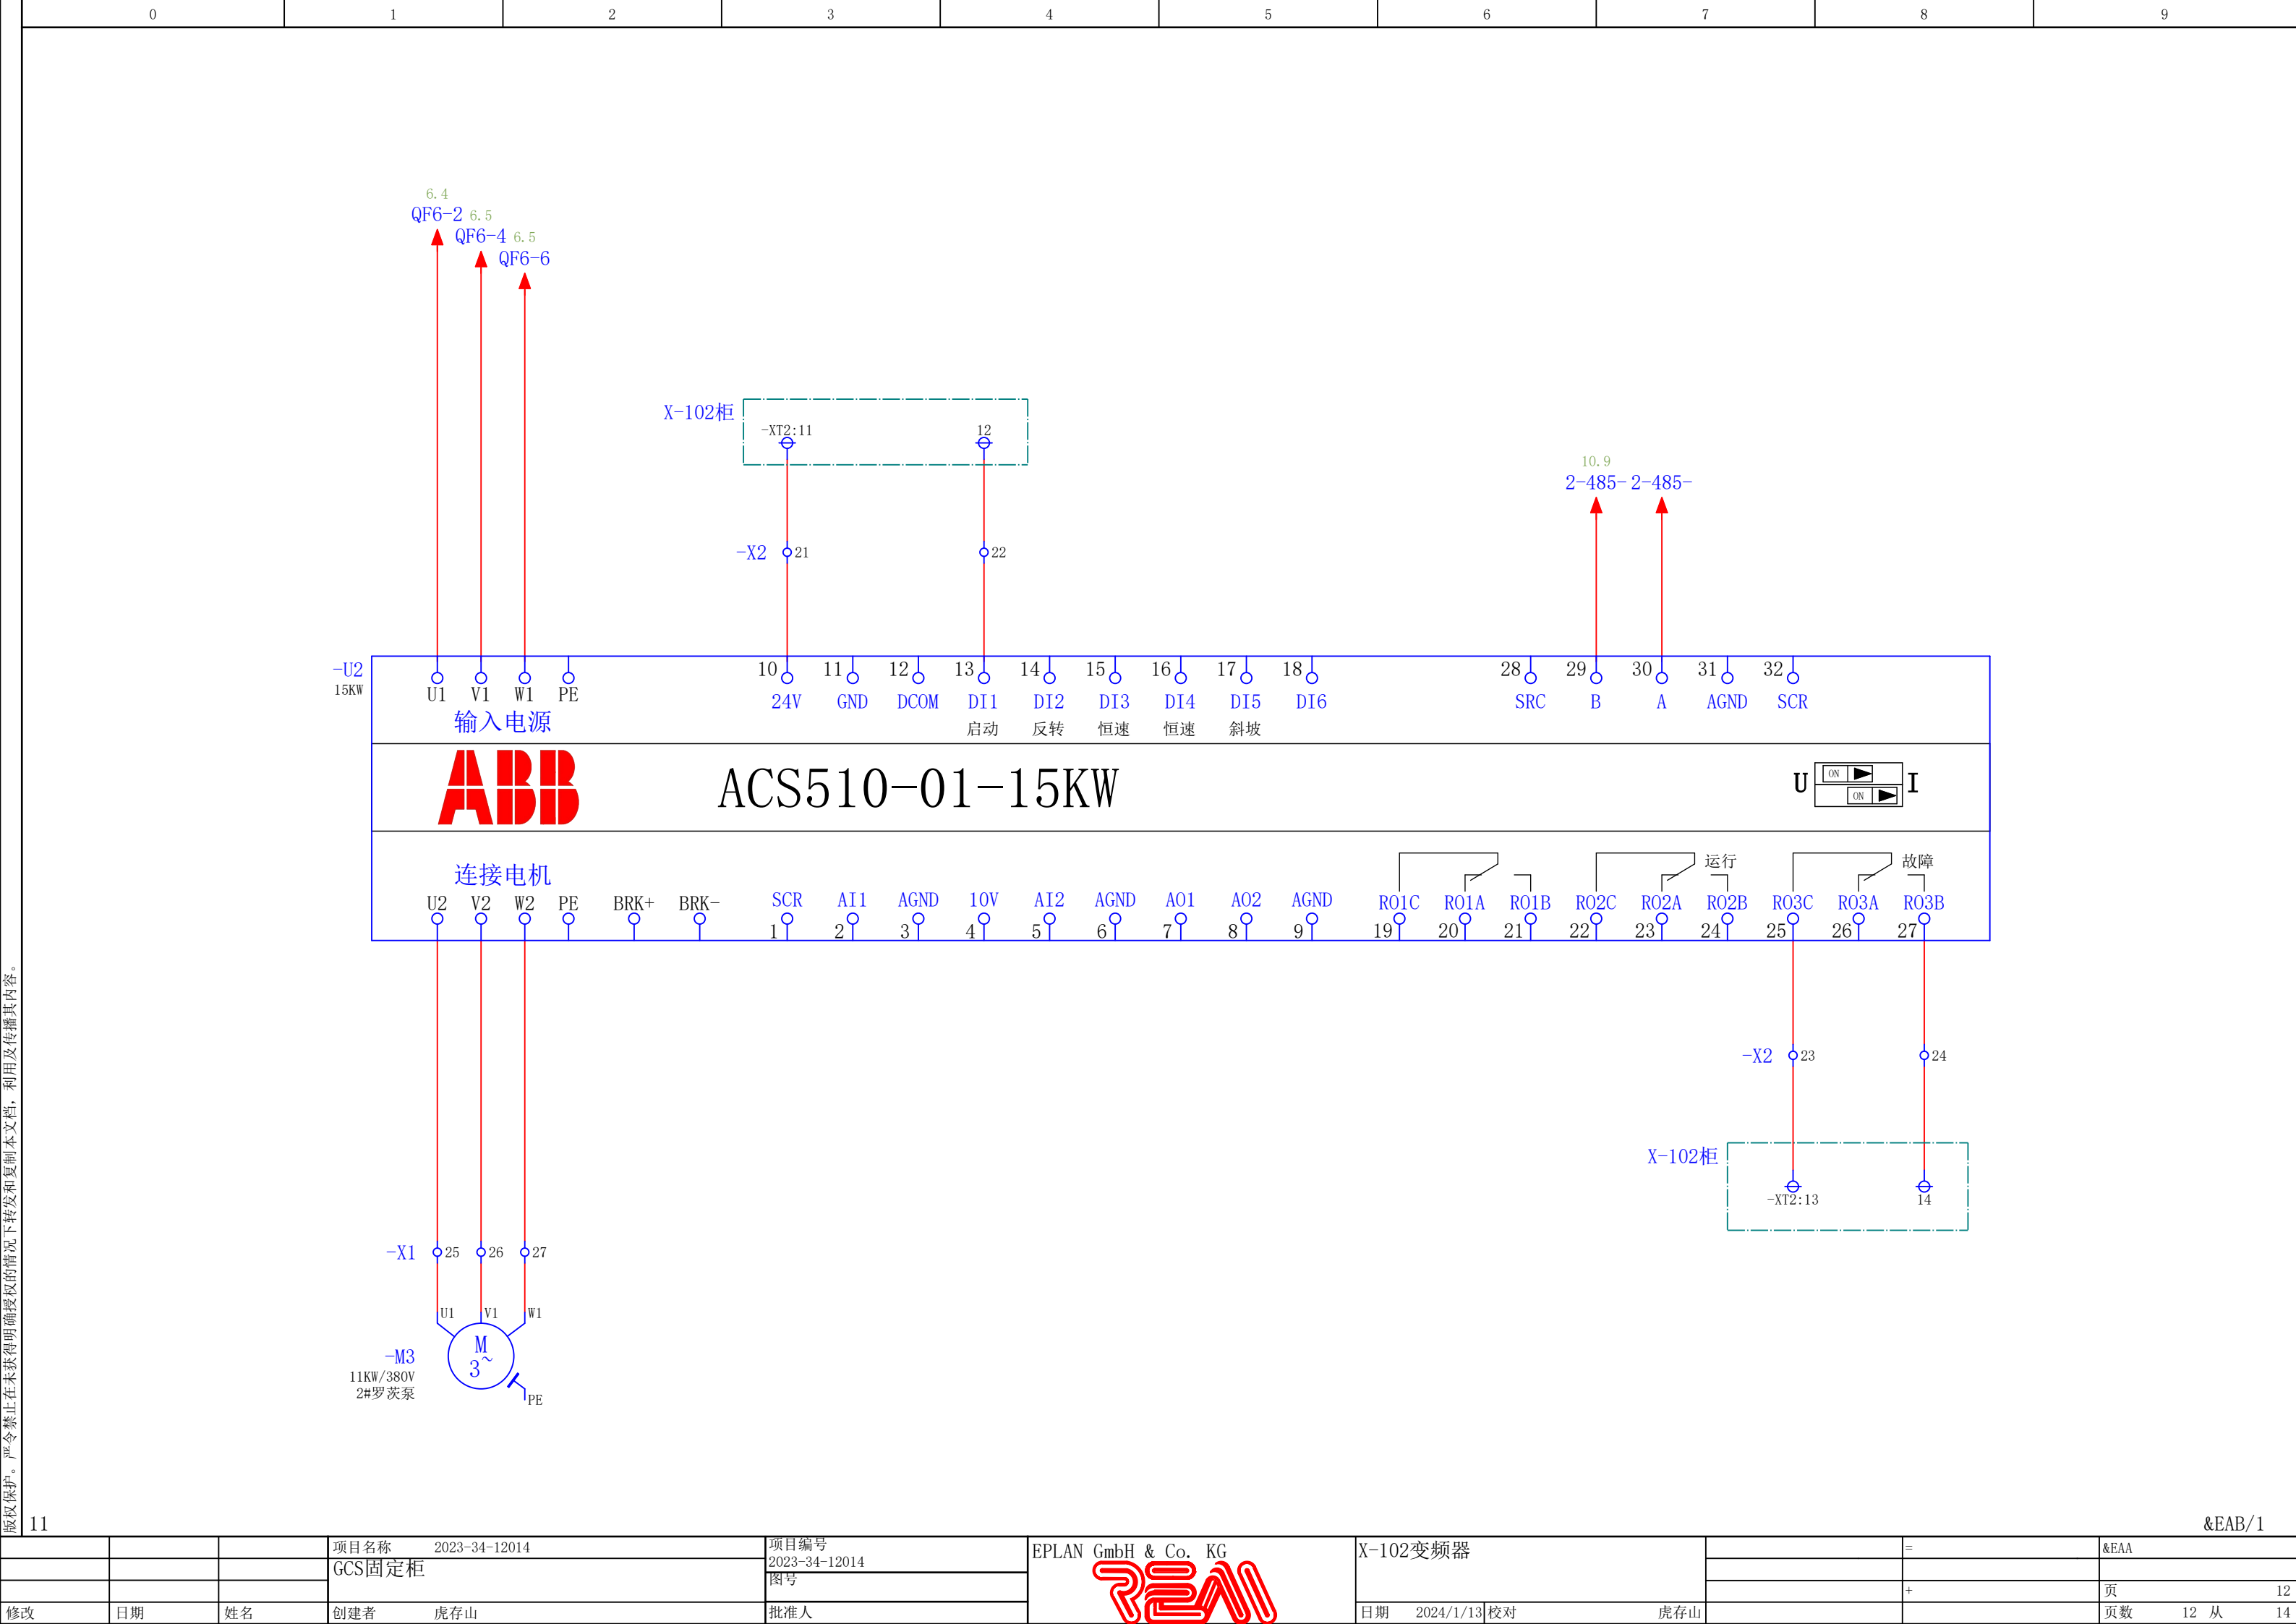

版权保护。严令禁止在未获得明确授权的情况下，转发和复制本文档，利用及传播其内容。

